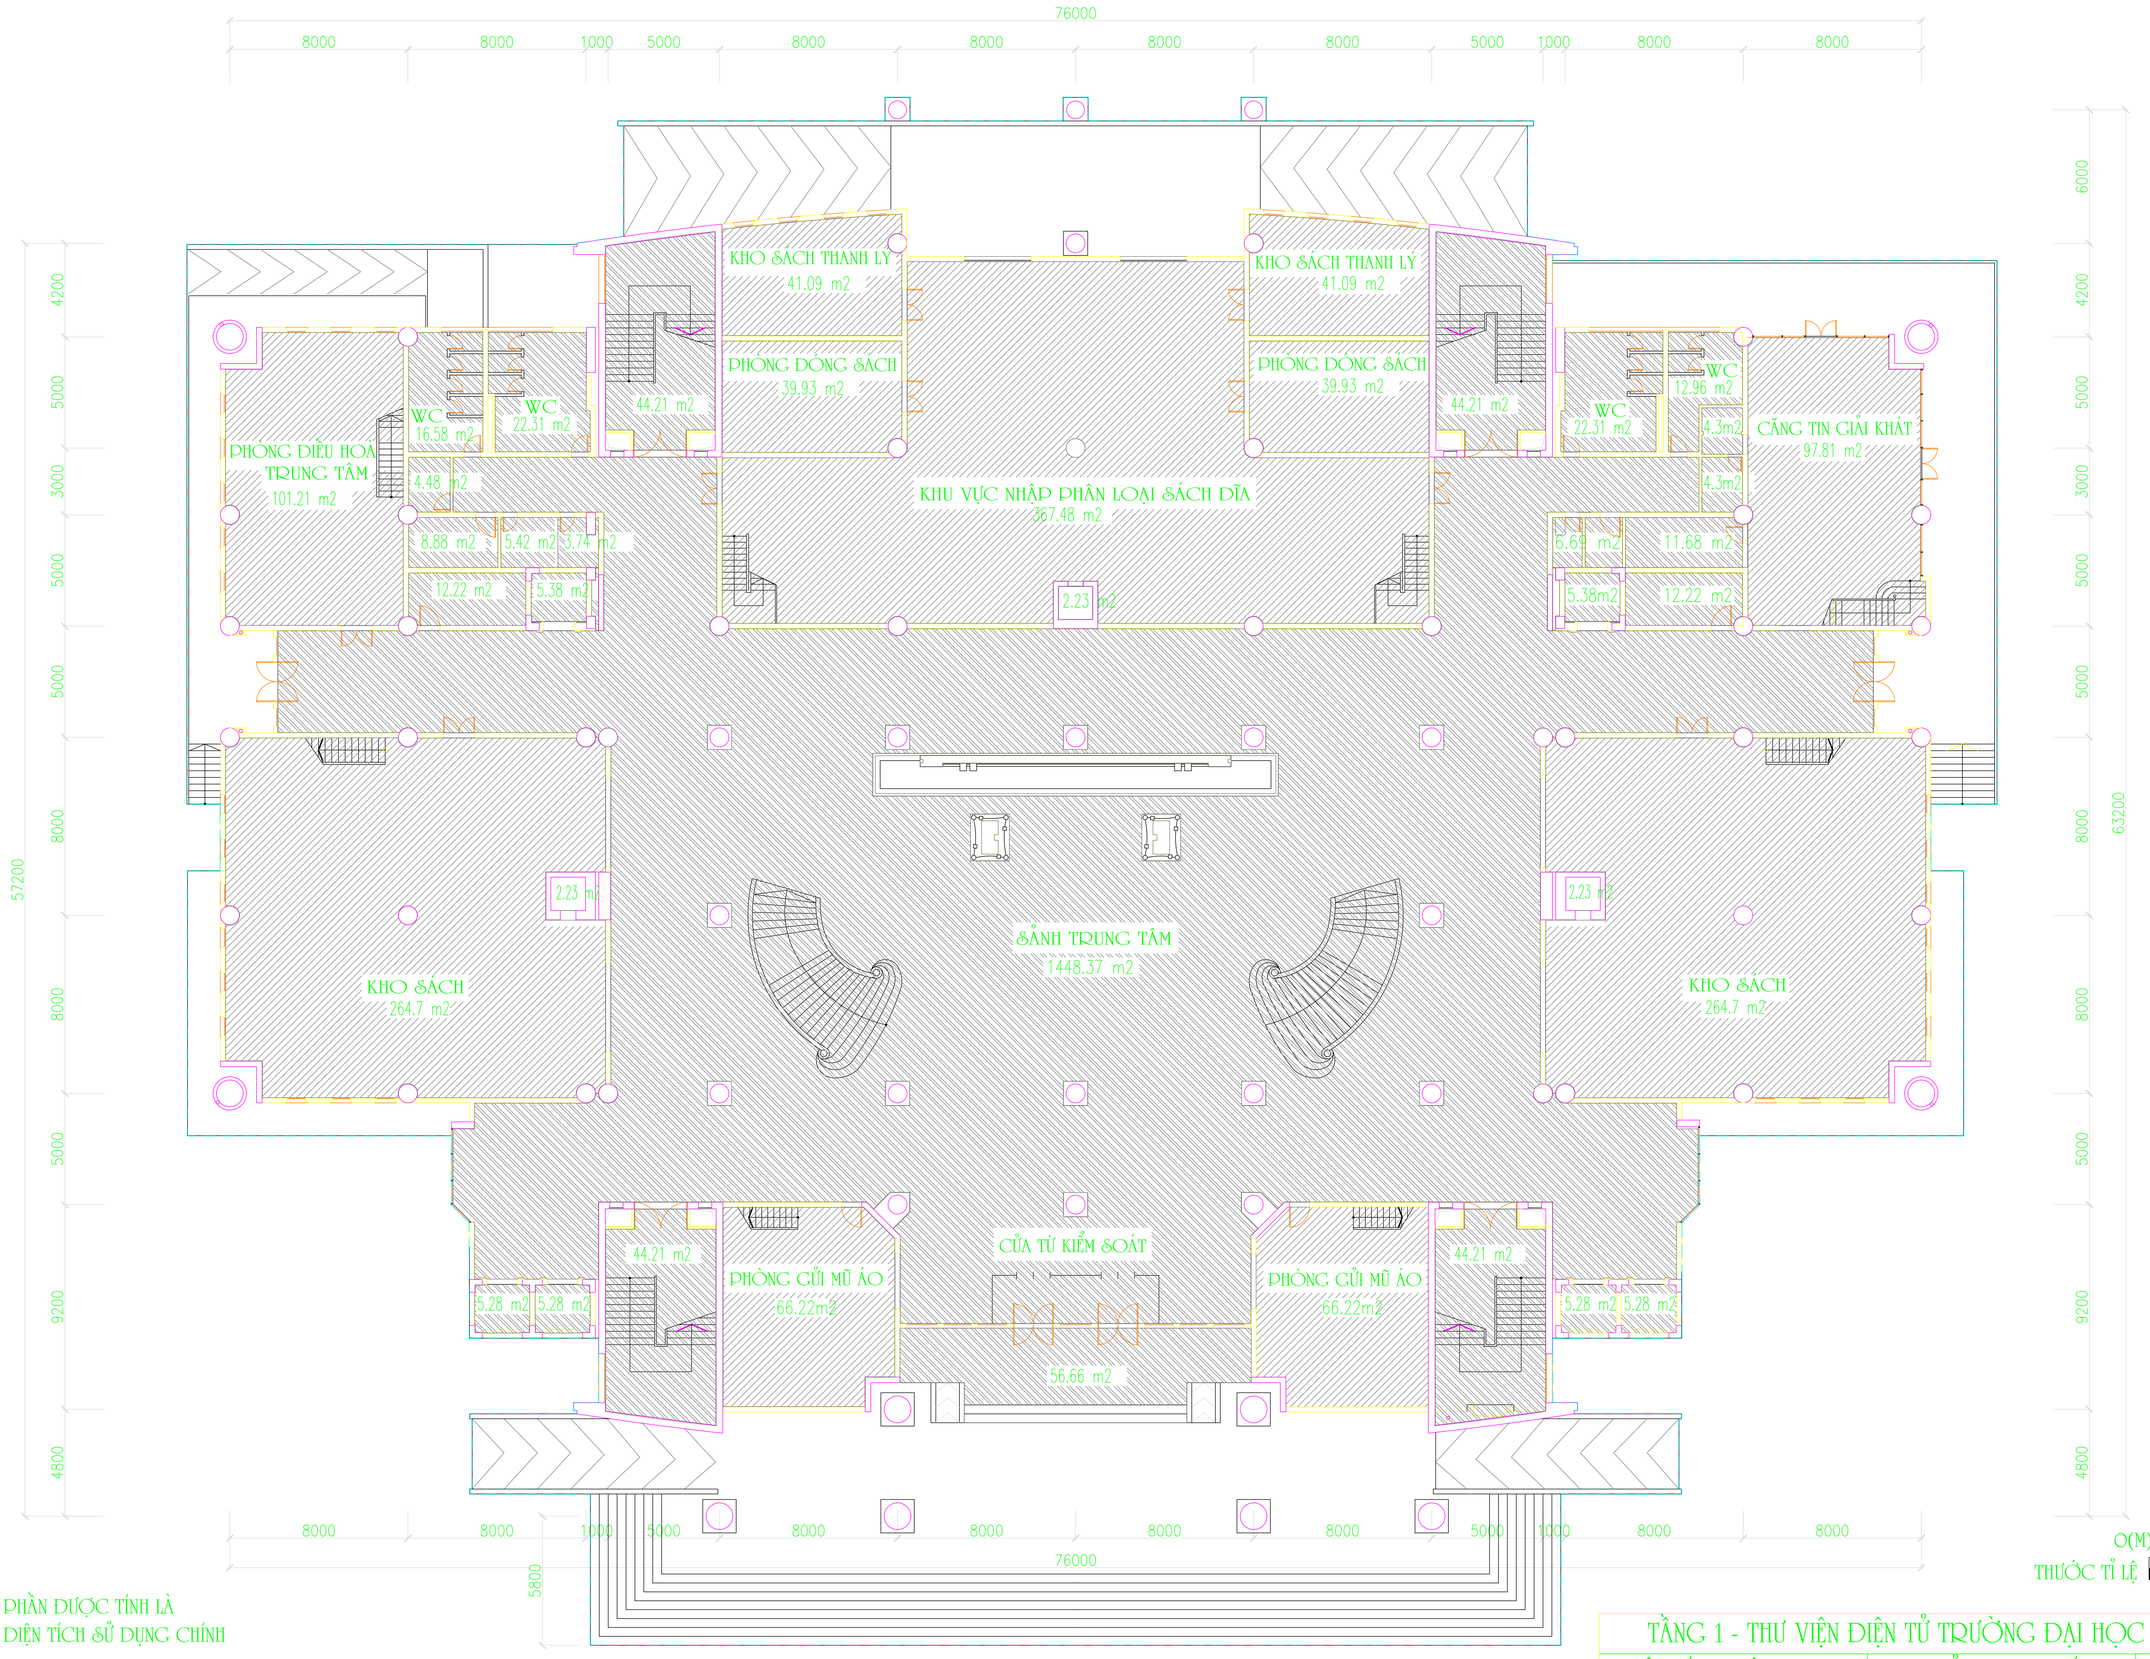


GHI CHÚ :

PHẦN ĐƯỢC TÍNH LÀ DIỆN TÍCH SỬ DỤNG CHÍNH

PHẦN ĐƯỢC TÍNH LÀ DIỆN TÍCH SỬ DỤNG PHỤ


MẶT BẰNG TẦNG 1

0(M) 1 3 6 10

THƯỚC TỈ LỆ

TẦNG 1 - THƯ VIỆN ĐIỆN TỬ TRƯỜNG ĐẠI HỌC BÁCH KHOA HÀ NỘI

DIỆN TÍCH XÂY DỰNG	DT SỬ DỤNG CHÍNH	DT SỬ DỤNG PHỤ	
		CẦU THANG, HÀNH LANG, SẢNH	KHU VỆ SINH VÀ KHO
4586.19 m2	1390.38 m2	2087.92 m2	148.09 m2
		2236.01 m2	

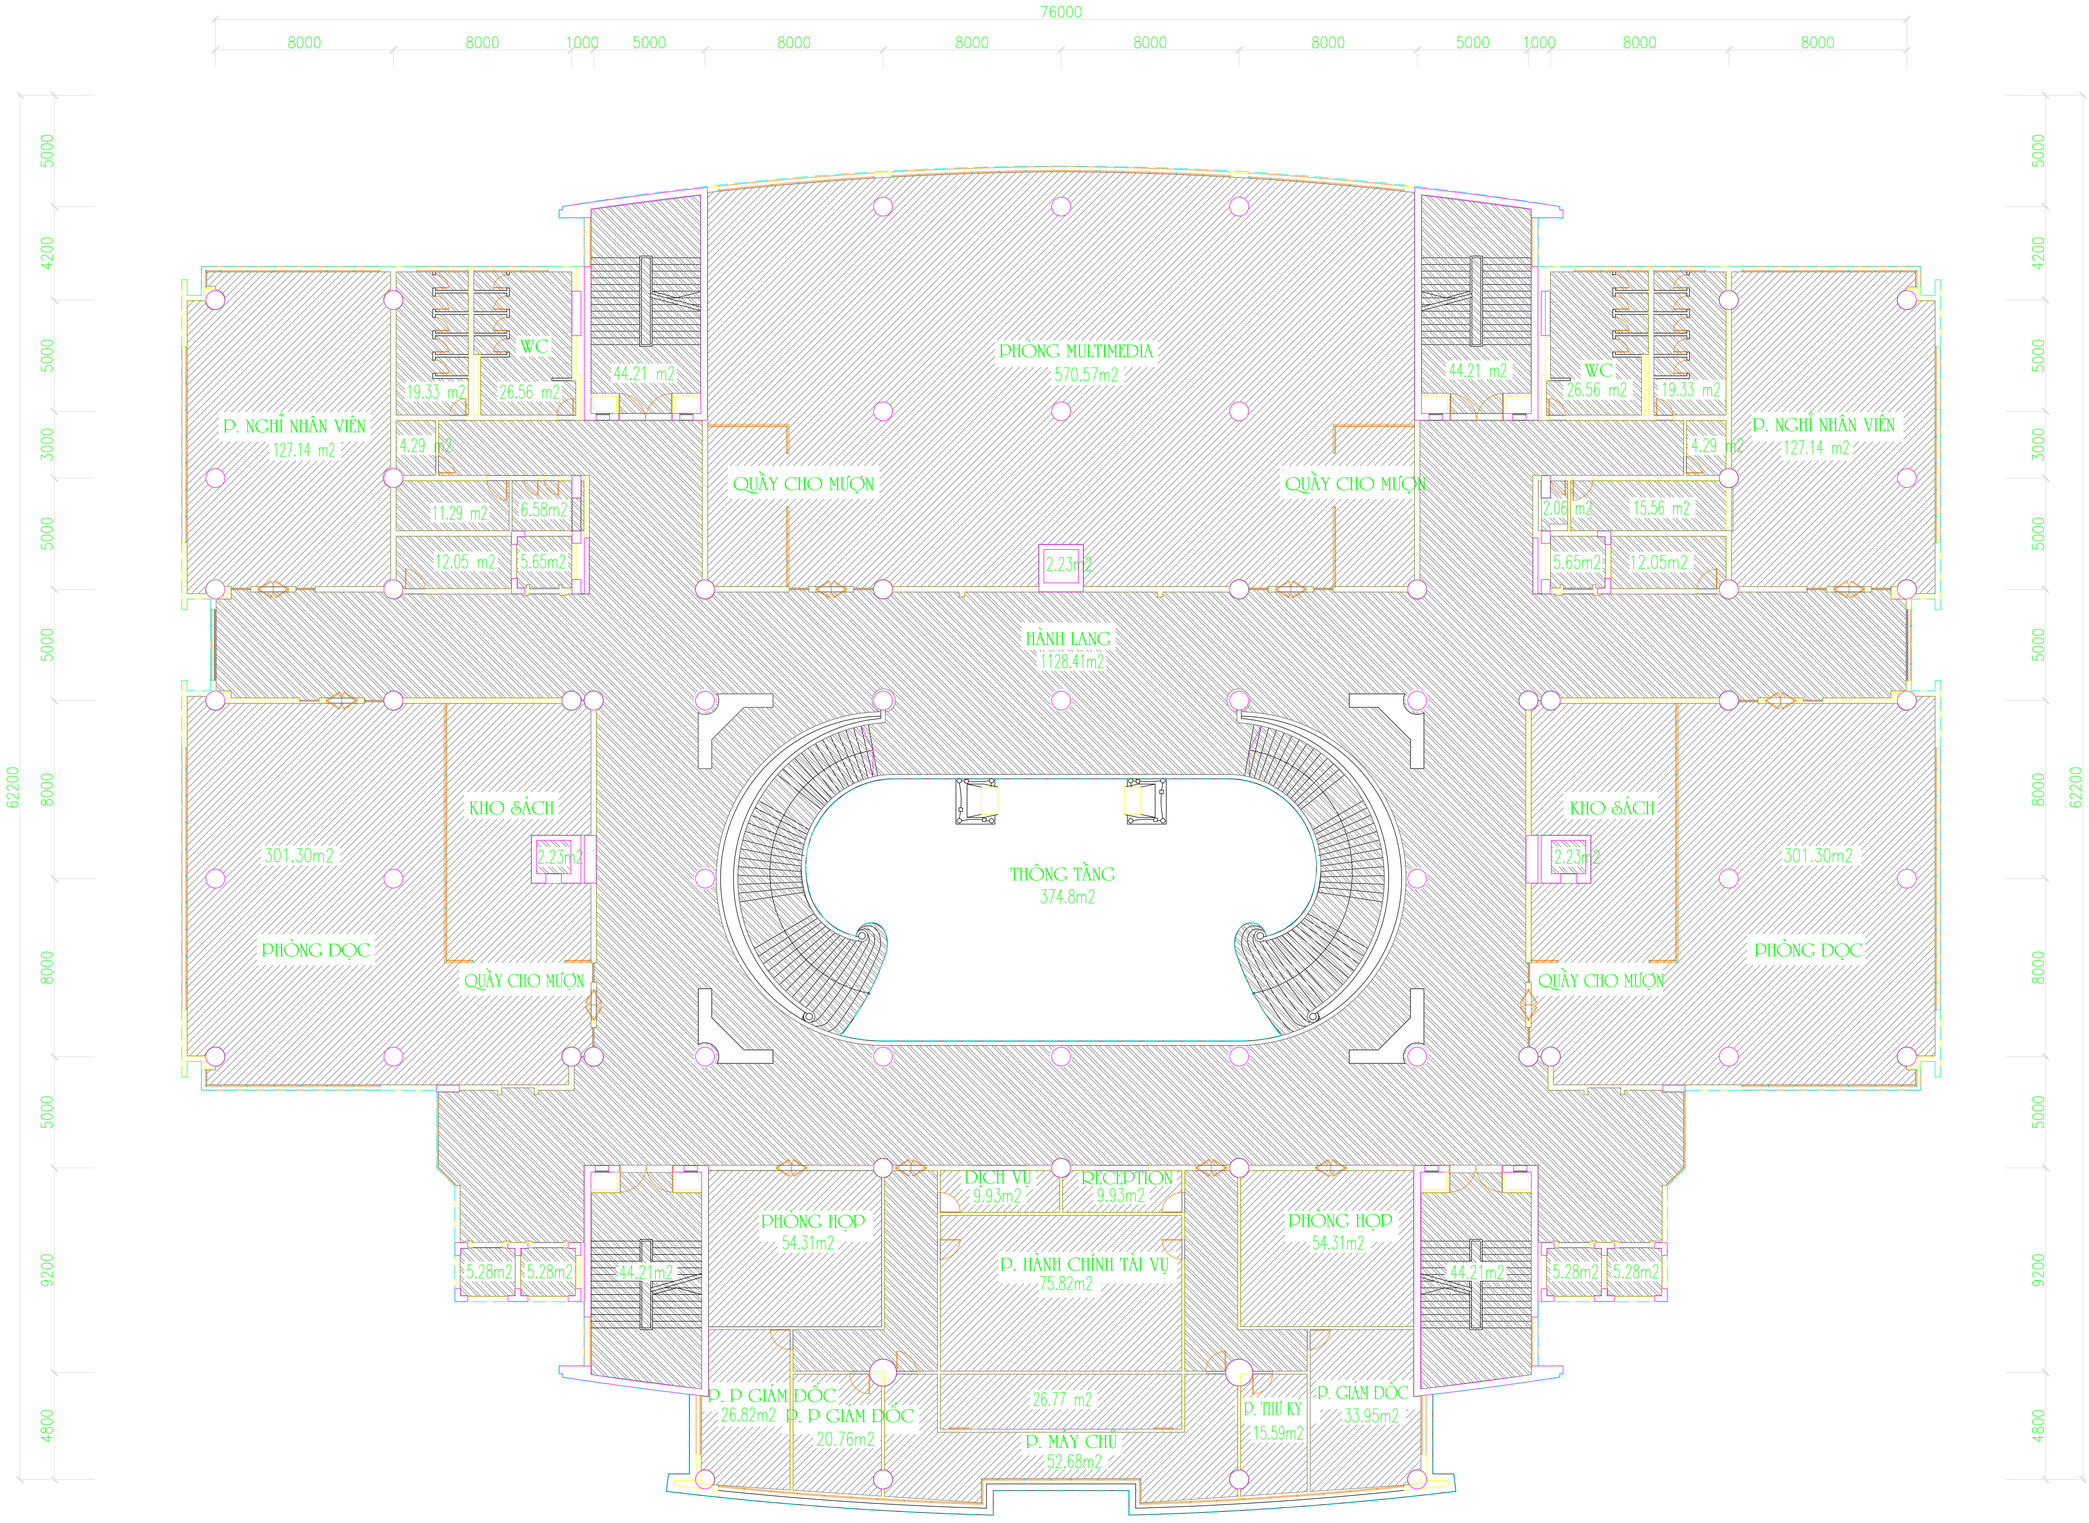

GHI CHÚ :

PHẦN ĐƯỢC TÍNH LÀ
DIỆN TÍCH SỬ DỤNG CHÍNH


PHẦN ĐƯỢC TÍNH LÀ
DIỆN TÍCH SỬ DỤNG PHỤ

O(M) 1 3 6 10
THƯỚC TỈ LỆ

MẶT BẰNG TẦNG 2

TẦNG 2- THƯ VIỆN ĐIỆN TỬ TRƯỜNG ĐẠI HỌC BÁCH KHOA HÀ NỘI

DIỆN TÍCH XÂY DỰNG	DT SỬ DỤNG CHÍNH	DT SỬ DỤNG PHỤ	
		CẦU THANG, HÀNH LANG, SẢNH	KHU VỆ SINH VÀ KHO
3719.54 m2	1808.32 m2	1344.36m2	159.95 m2
		1504.31m2	

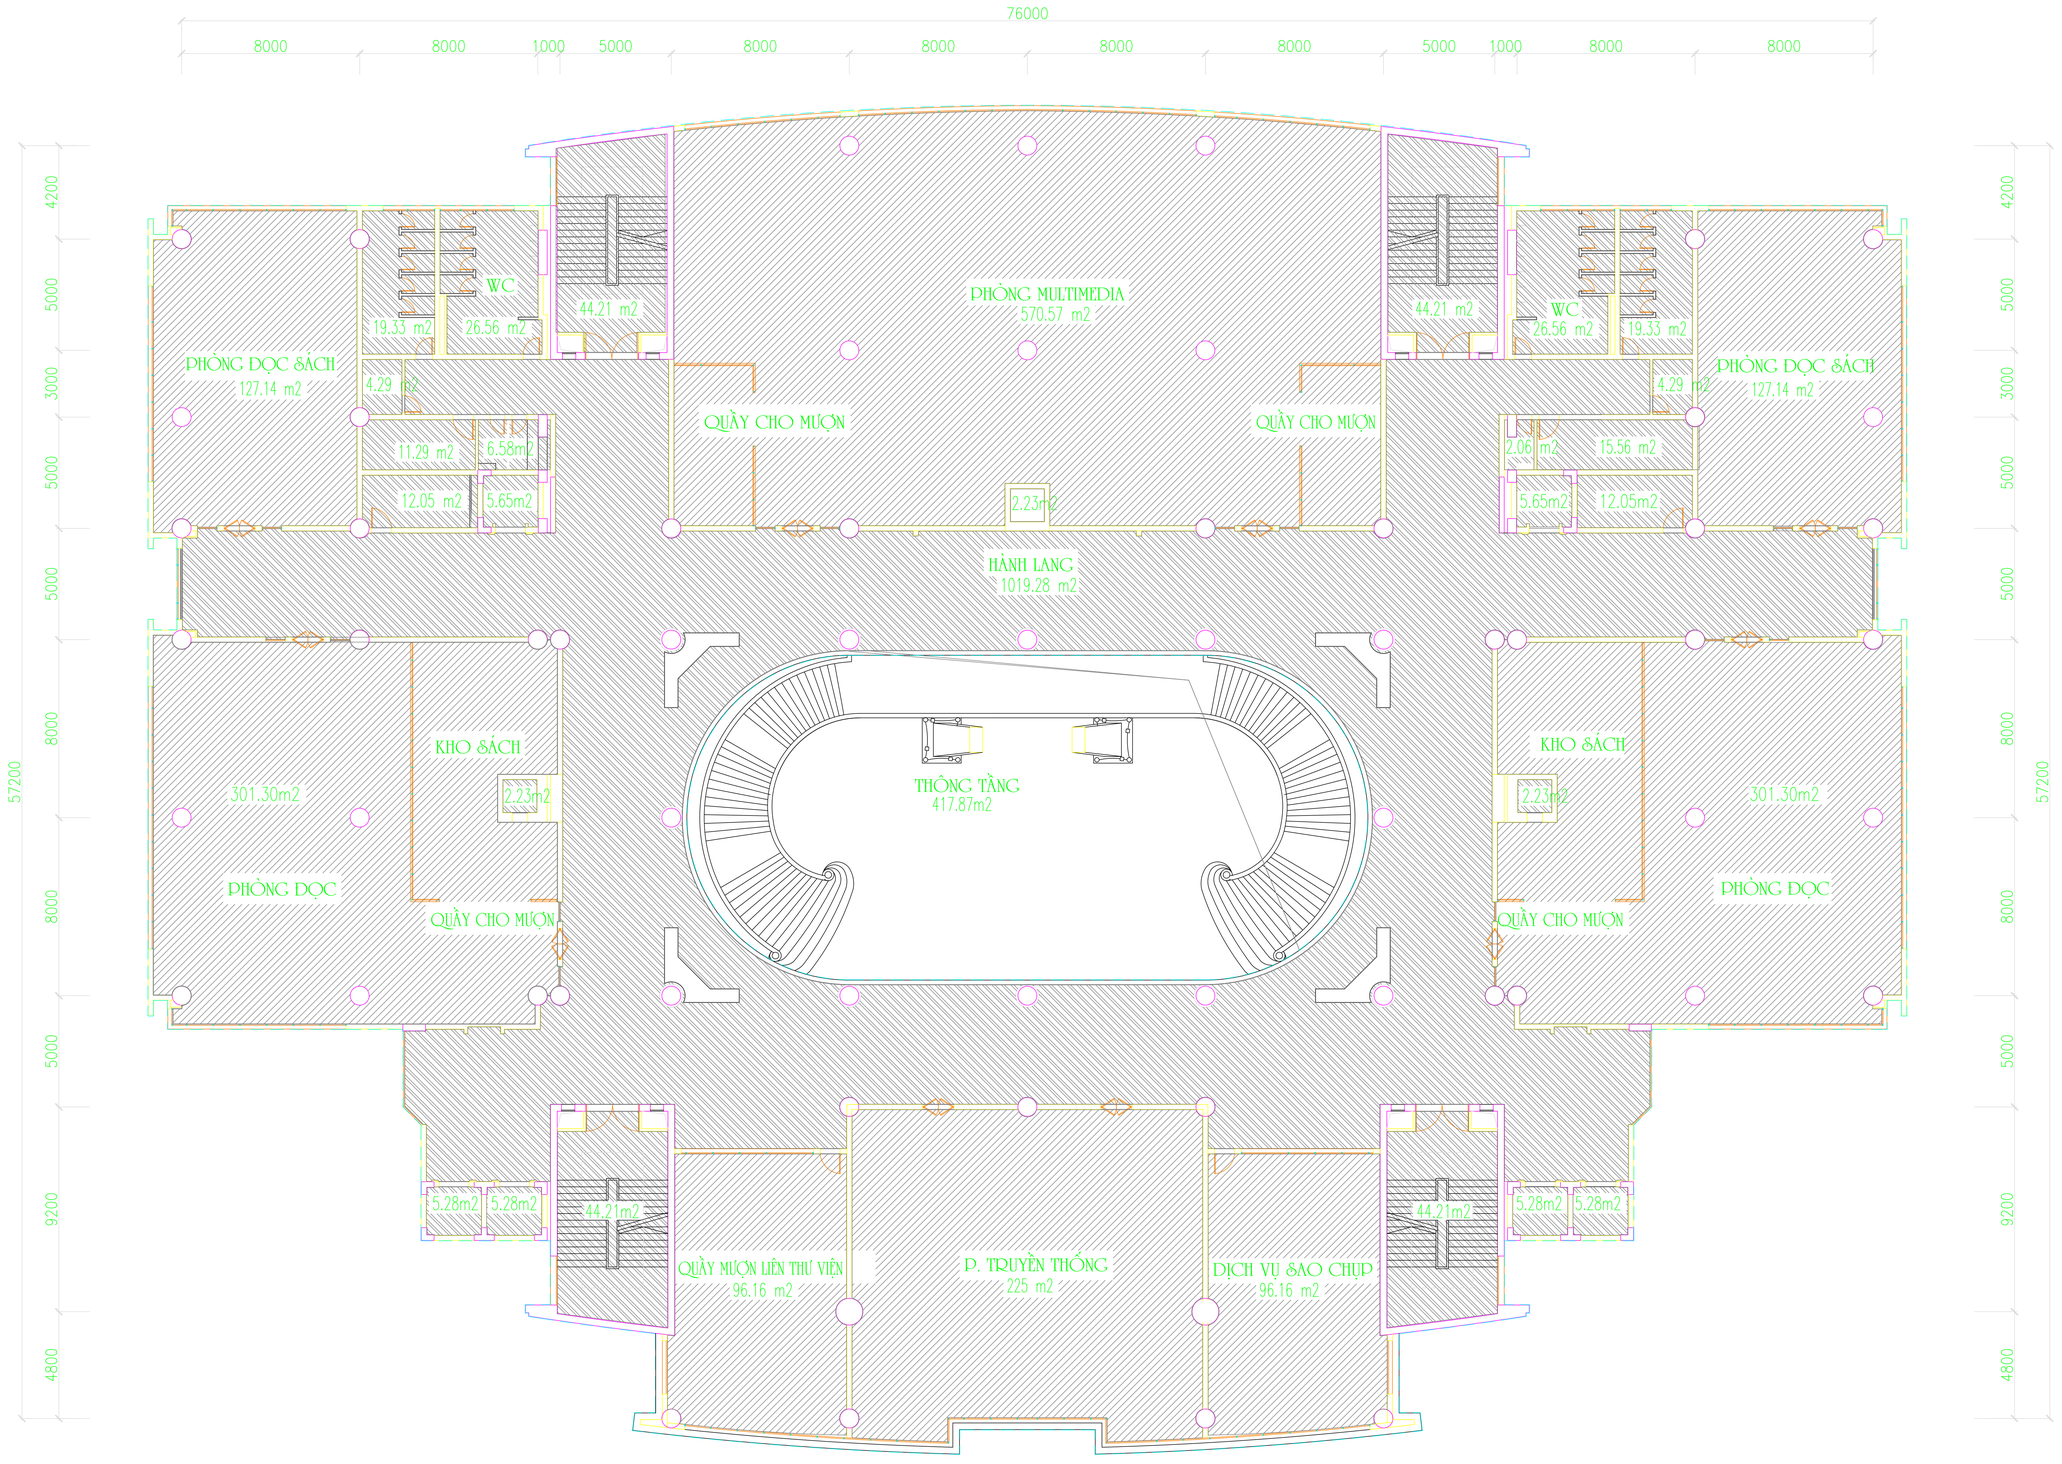

GHI CHÚ :

PHẦN ĐƯỢC TÍNH LÀ
DIỆN TÍCH SỬ DỤNG CHÍNH


PHẦN ĐƯỢC TÍNH LÀ
DIỆN TÍCH SỬ DỤNG PHỤ

MẶT BẰNG TẦNG 3

O(M) 1 3 6 10
THƯỚC TỈ LỆ

TẦNG 3 - THƯ VIỆN ĐIỆN TỬ TRƯỜNG ĐẠI HỌC BÁCH KHOA HÀ NỘI

DIỆN TÍCH XÂY DỰNG	DT SỬ DỤNG CHÍNH	DT SỬ DỤNG PHỤ	
		CẦU THANG, HÀNH LANG, SẢNH	KHU VỆ SINH VÀ KHO
3550.89 m2	1844.77 m2	1235.23 m2	159.95 m2
		1395.18 m2	

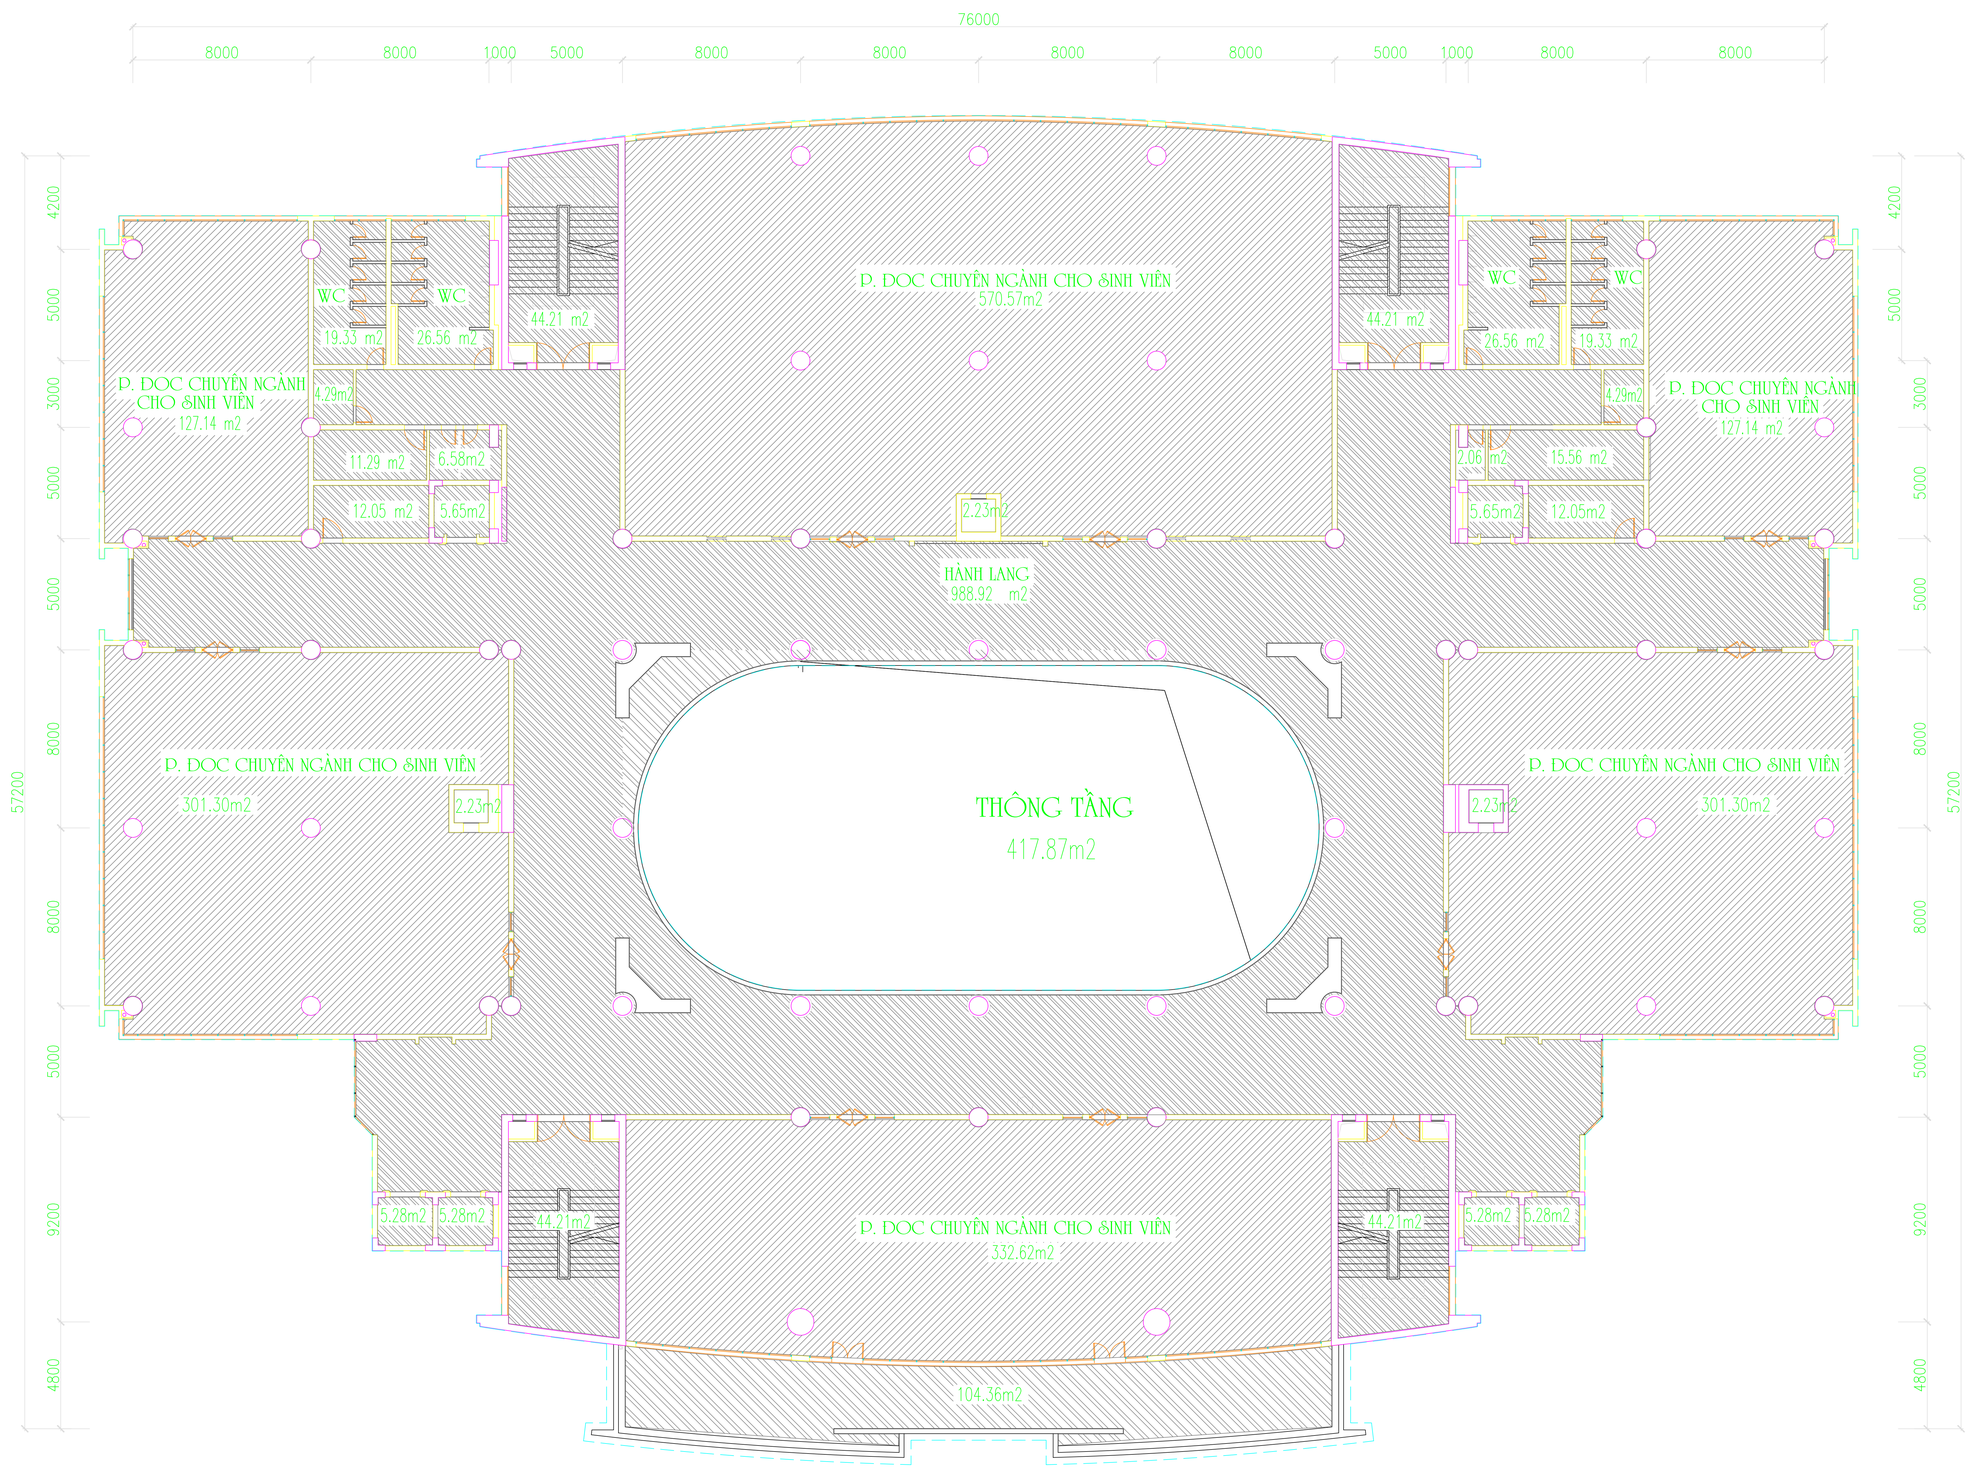


GHI CHÚ :

phÇn ??# tÝnh !µ

DIỆN TÍCH SỬ DỤNG CHÍNH

PHẦN ĐƯỢC TÍNH LÀ
DIỆN TÍCH SỬ DỤNG PHỤ

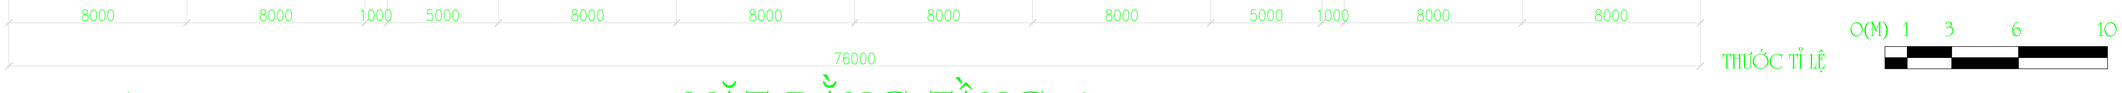


THƯỚC TỈ LỆ

O(M) 1 3 6 10

MẶT BẰNG TẦNG 4

TẦNG 4 - THƯ VIỆN ĐIỆN TỬ TRƯỜNG ĐẠI HỌC BÁCH KHOA HÀ NỘI

DIỆN TÍCH XÂY DỰNG	DT SỬ DỤNG CHÍNH	DT SỬ DỤNG PHỤ	
		CẦU THANG, HÀNH LANG, SẢNH	KHU VỆ SINH VÀ KHO
3550.89 m2	1760.07m2	1309.23 m2	159.95 m2
		1469.18 m2	

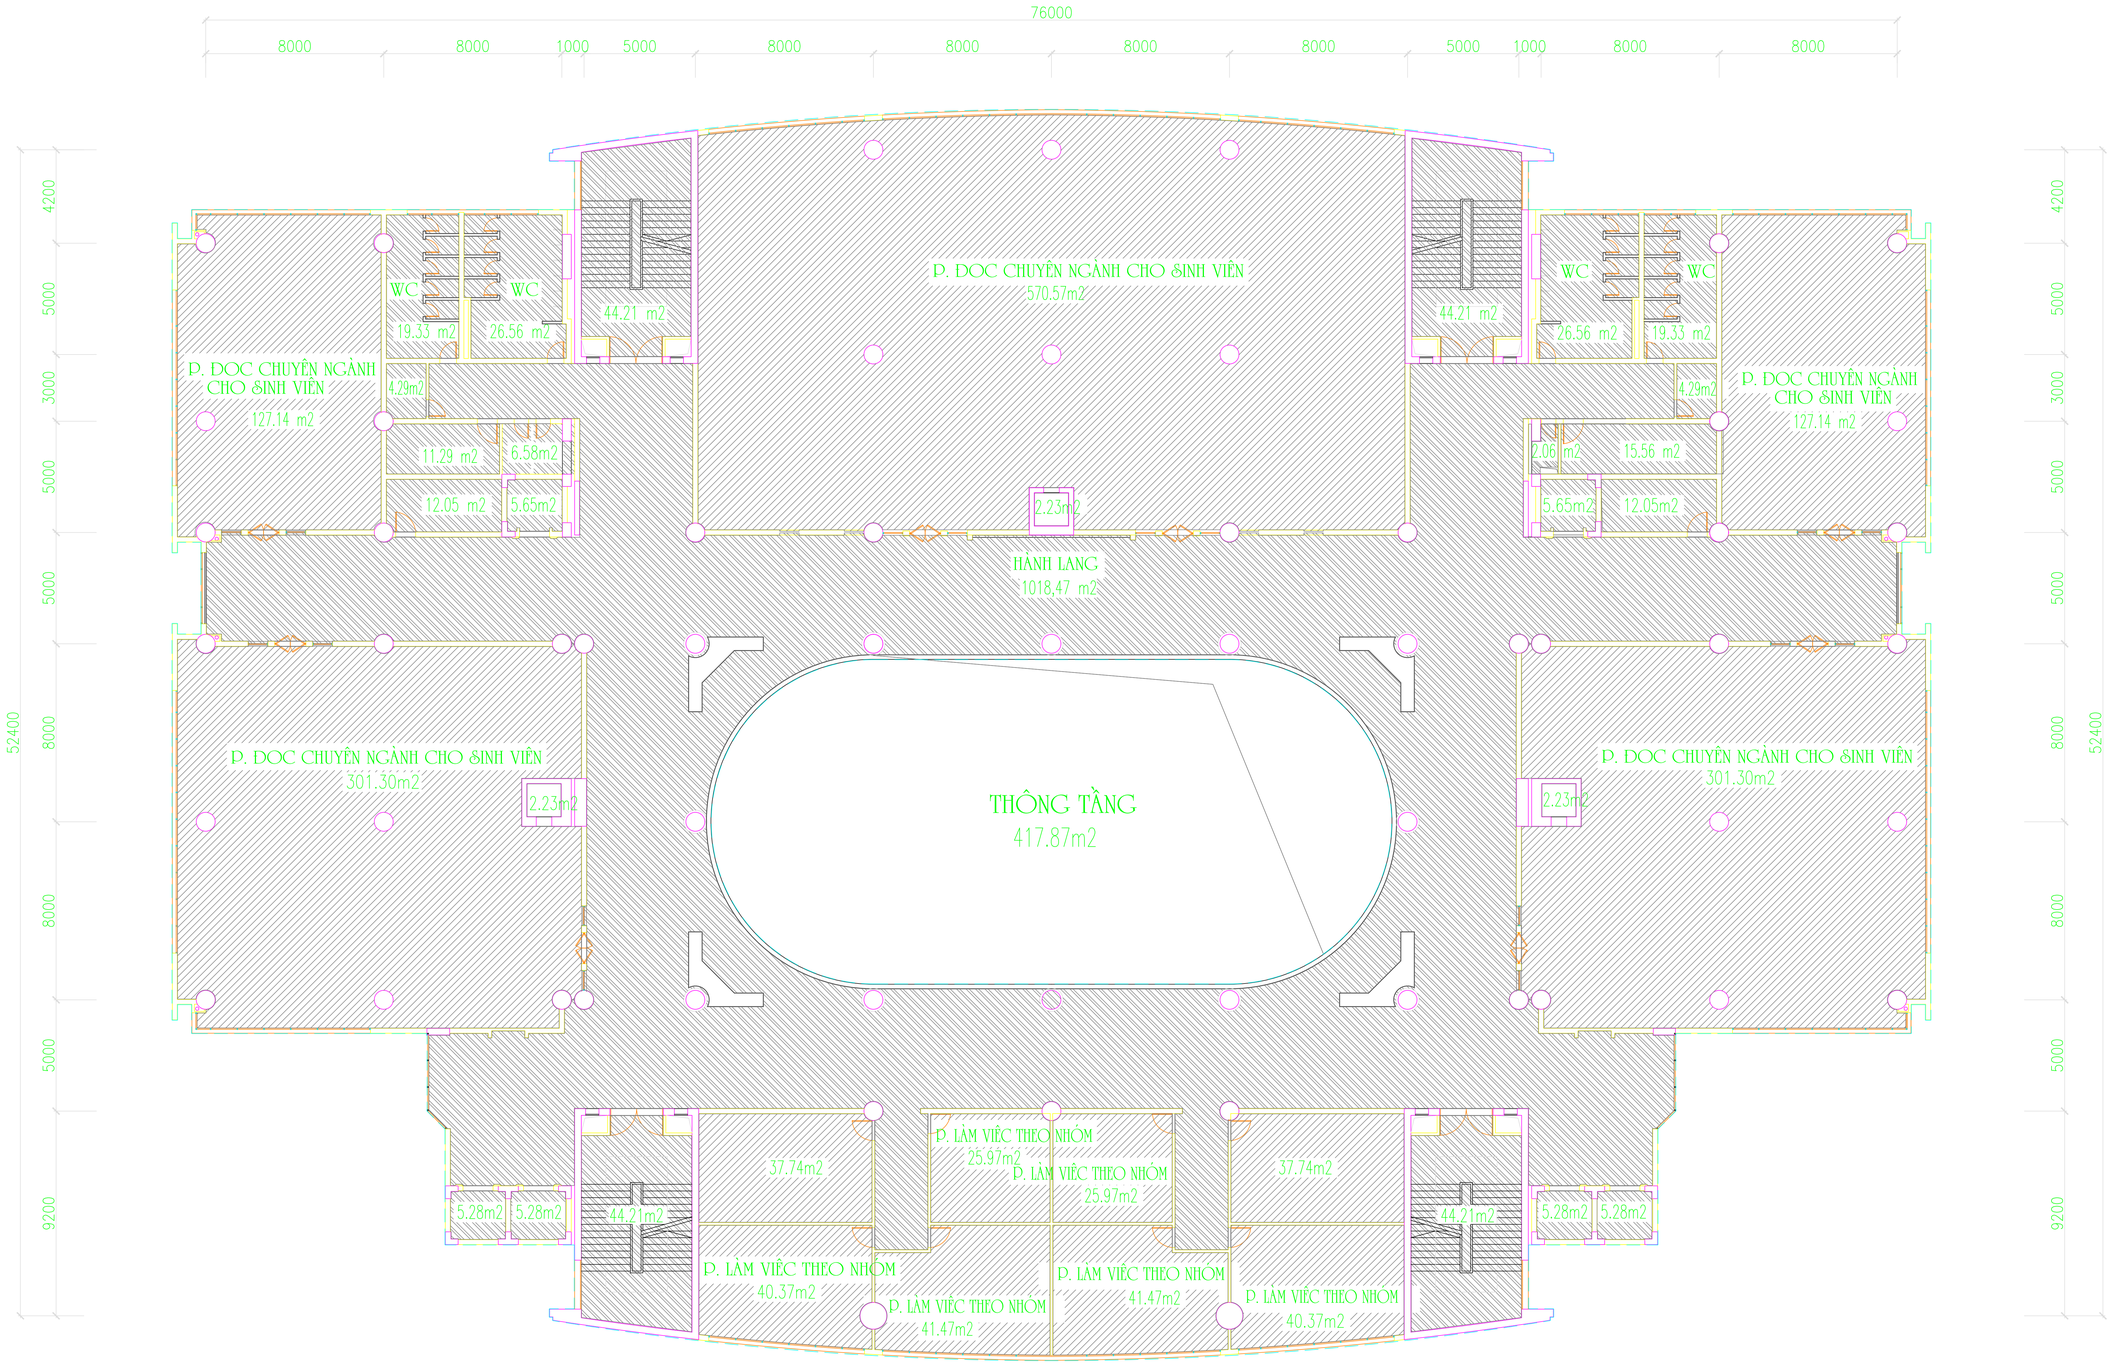

GHI CHÚ :

PHẦN ĐƯỢC TÍNH LÀ
DIỆN TÍCH SỬ DỤNG CHÍNH


PHẦN ĐƯỢC TÍNH LÀ
DIỆN TÍCH SỬ DỤNG PHỤ

MẶT BẰNG TẦNG 5

THƯỚC TỈ LỆ 0(M) 1 3 6 10

TẦNG 5 - THƯ VIỆN ĐIỆN TỬ TRƯỜNG ĐẠI HỌC BÁCH KHOA HÀ NỘI

DIỆN TÍCH XÂY DỰNG	DT SỬ DỤNG CHÍNH	DT SỬ DỤNG PHỤ	
		CẦU THANG, HÀNH LANG, SẢNH	KHU VỆ SINH VÀ KHO
3408.03 m2	1718.55m2	1234.42 m2	159.95 m2
		1394.37 m2	

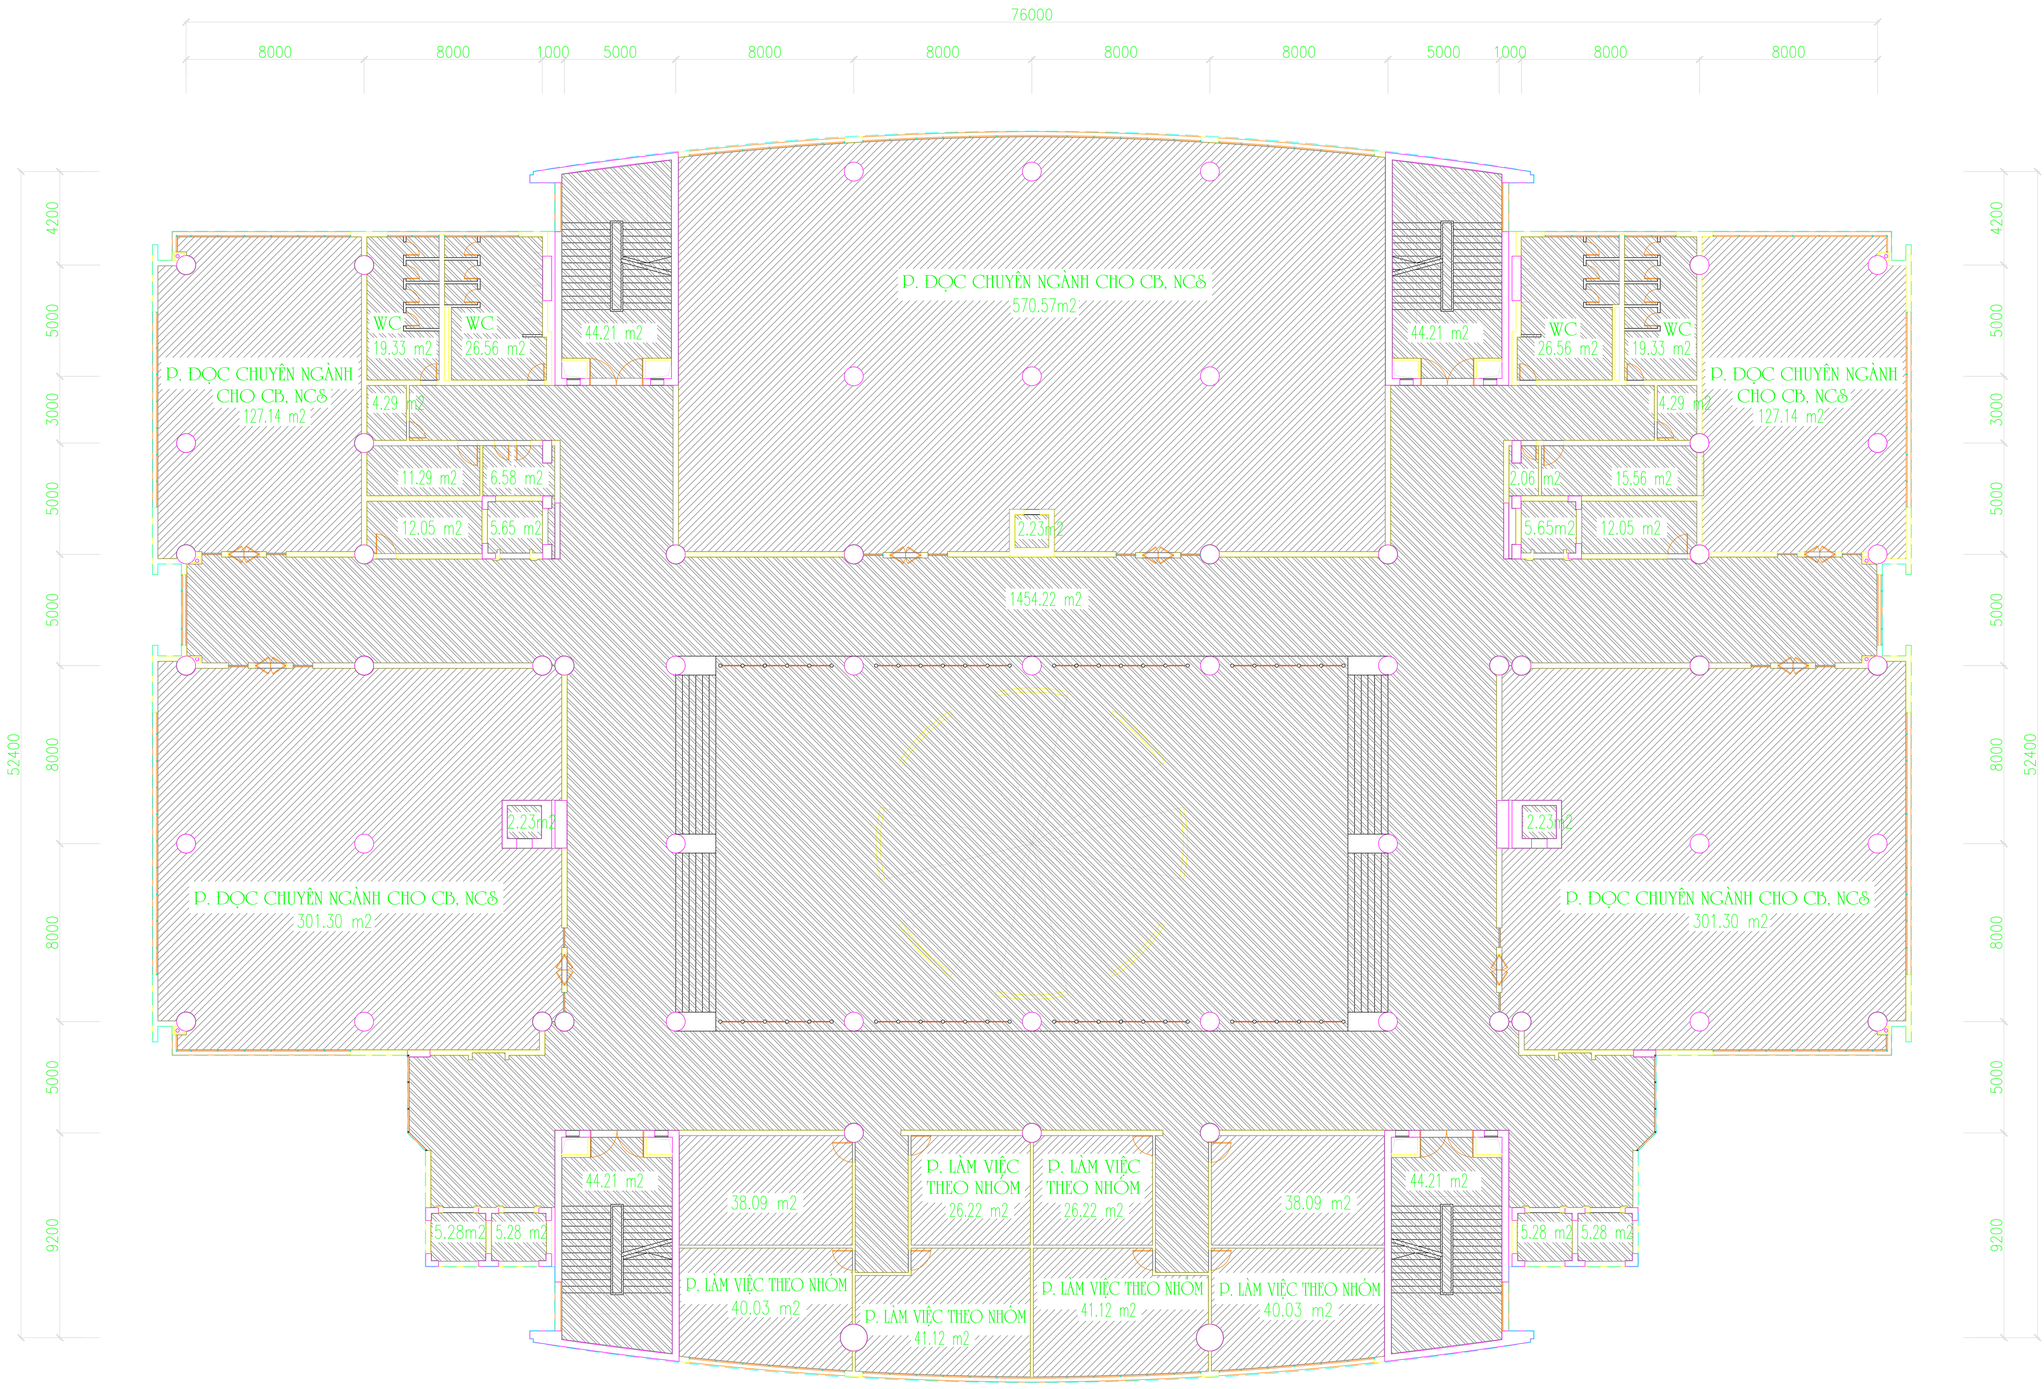

GHI CHÚ :

PHẦN ĐƯỢC TÍNH LÀ
DIỆN TÍCH SỬ DỤNG CHÍNH


PHẦN ĐƯỢC TÍNH LÀ
DIỆN TÍCH SỬ DỤNG PHỤ

MẶT BẰNG TẦNG 6

0(M) 1 3 6 10
THƯỚC TỈ LỆ

TẦNG 6 - THƯ VIỆN ĐIỆN TỬ TRƯỜNG ĐẠI HỌC BÁCH KHOA HÀ NỘI

DIỆN TÍCH XÂY DỰNG	DT SỬ DỤNG CHÍNH	DT SỬ DỤNG PHỤ	
		CẦU THANG, HÀNH LANG, SẢNH	KHU VỆ SINH VÀ KHO
3807.88 m2	1718.05 m2	1670.17 m2	159.95 m2
		1818.82 m2	

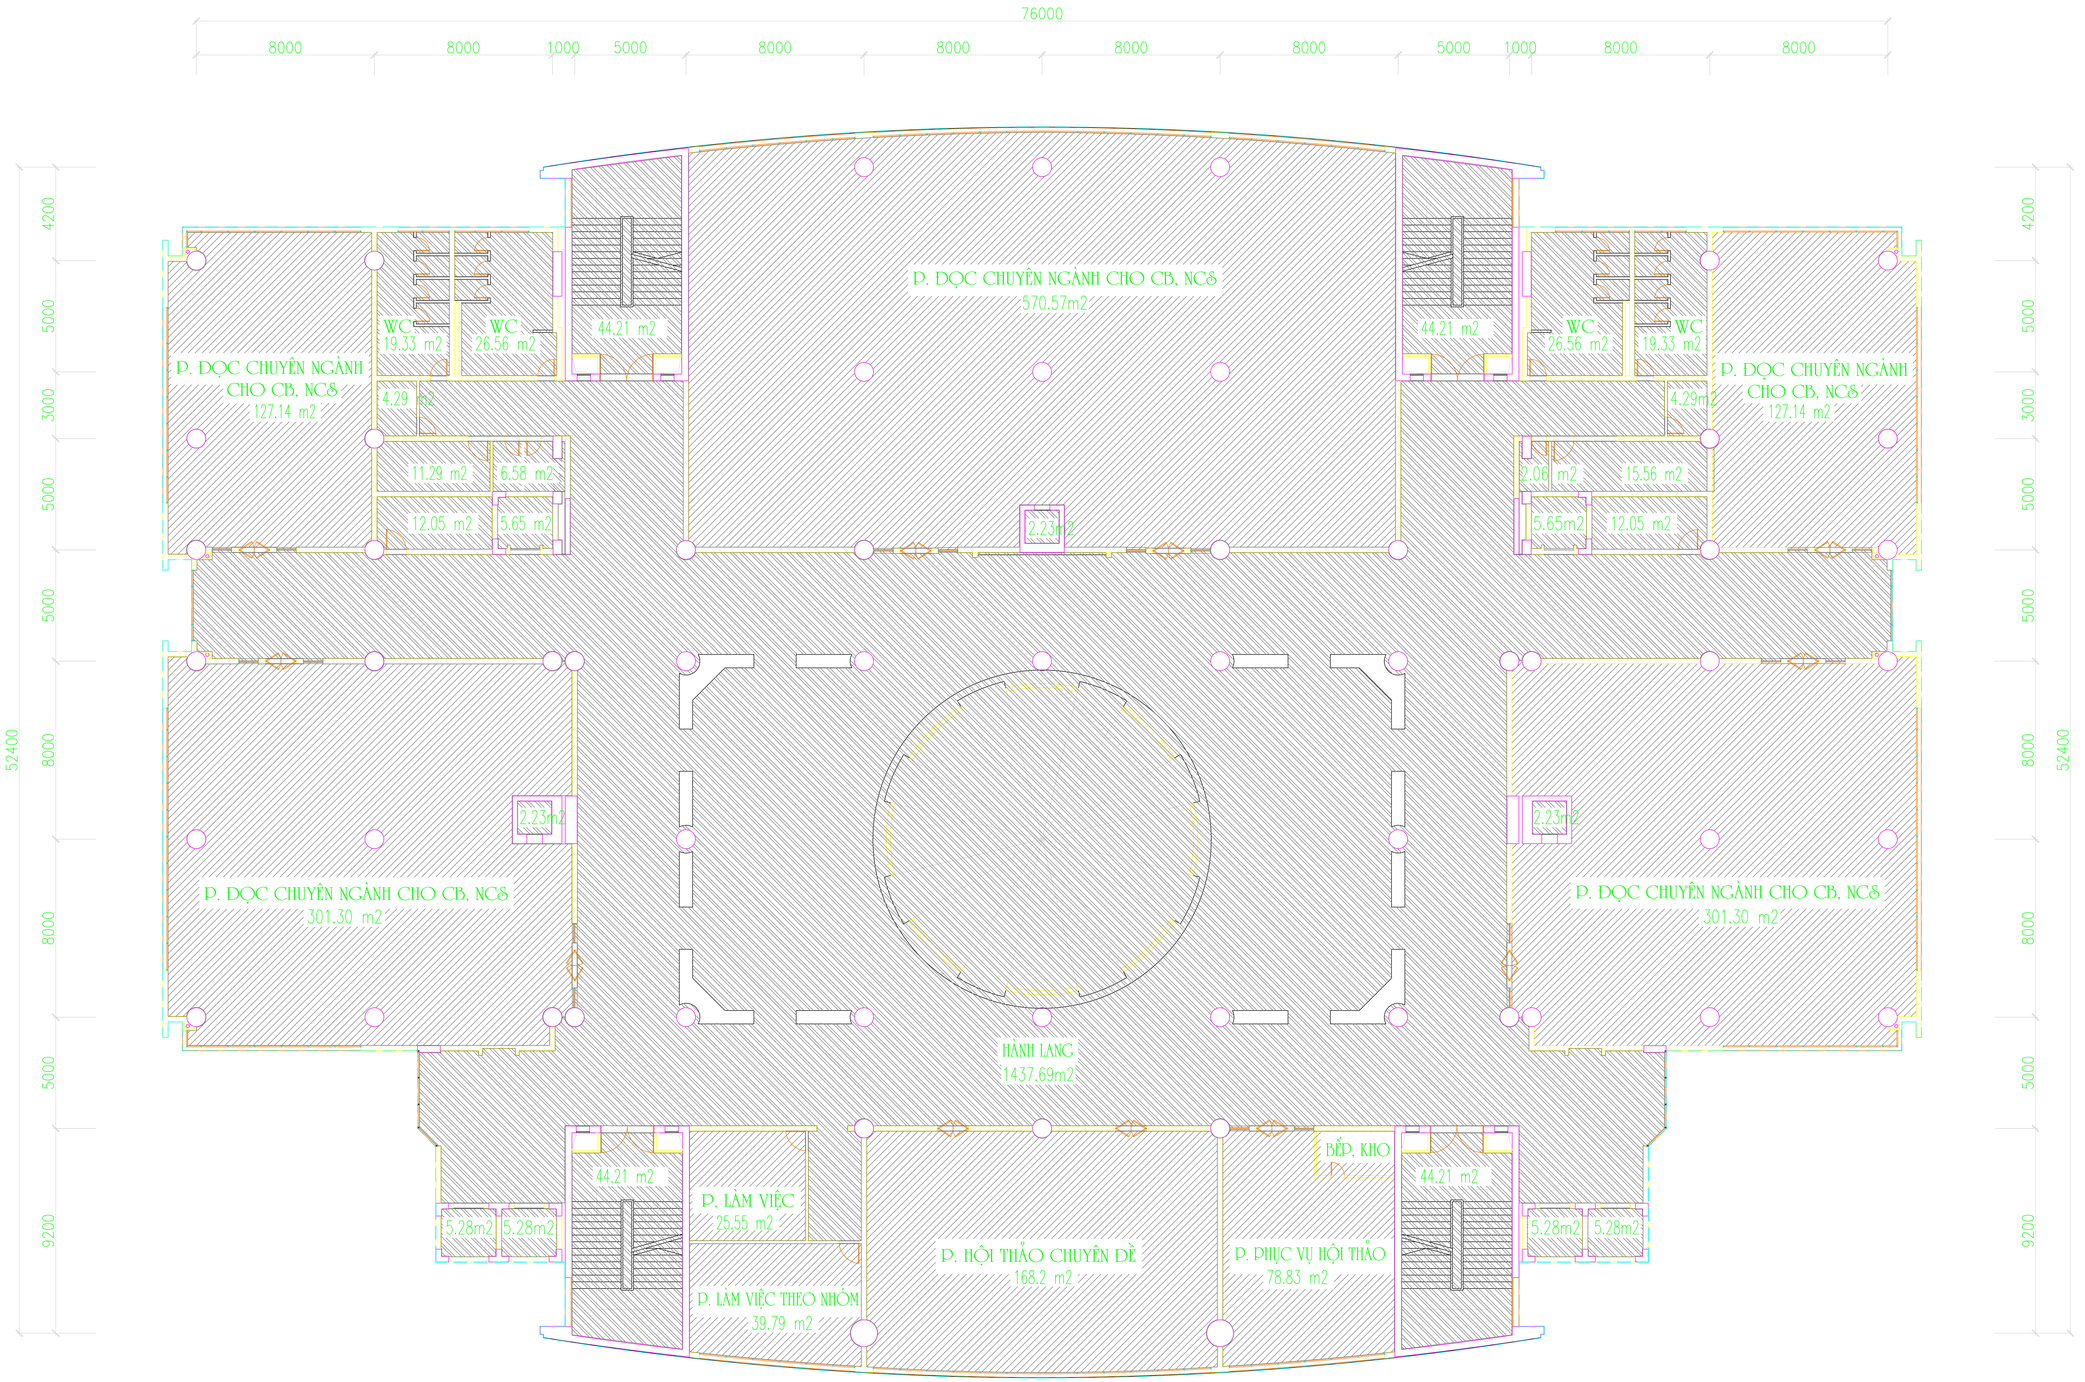

8000 8000 1000 5000 8000 8000 8000 8000 5000 1000 8000 8000
76000

0(M) 1 3 6 10

THƯỚC TỈ LỆ

GHI CHÚ :


PHẦN ĐƯỢC TÍNH LÀ
DIỆN TÍCH SỬ DỤNG CHÍNH

PHẦN ĐƯỢC TÍNH LÀ
DIỆN TÍCH SỬ DỤNG PHỤ

MẶT BẰNG TẦNG 7

TẦNG 7 - THƯ VIỆN ĐIỆN TỬ TRƯỜNG ĐẠI HỌC BÁCH KHOA HÀ NỘI

DIỆN TÍCH XÂY DỰNG	DT SỬ DỤNG CHÍNH	DT SỬ DỤNG PHỤ	
		CẦU THANG, HÀNH LANG, SẢNH	KHU VỆ SINH VÀ KHO
3807.88 m2	1739.50 m2	1653.64 m2	159.95 m2
		1802.29 m2	

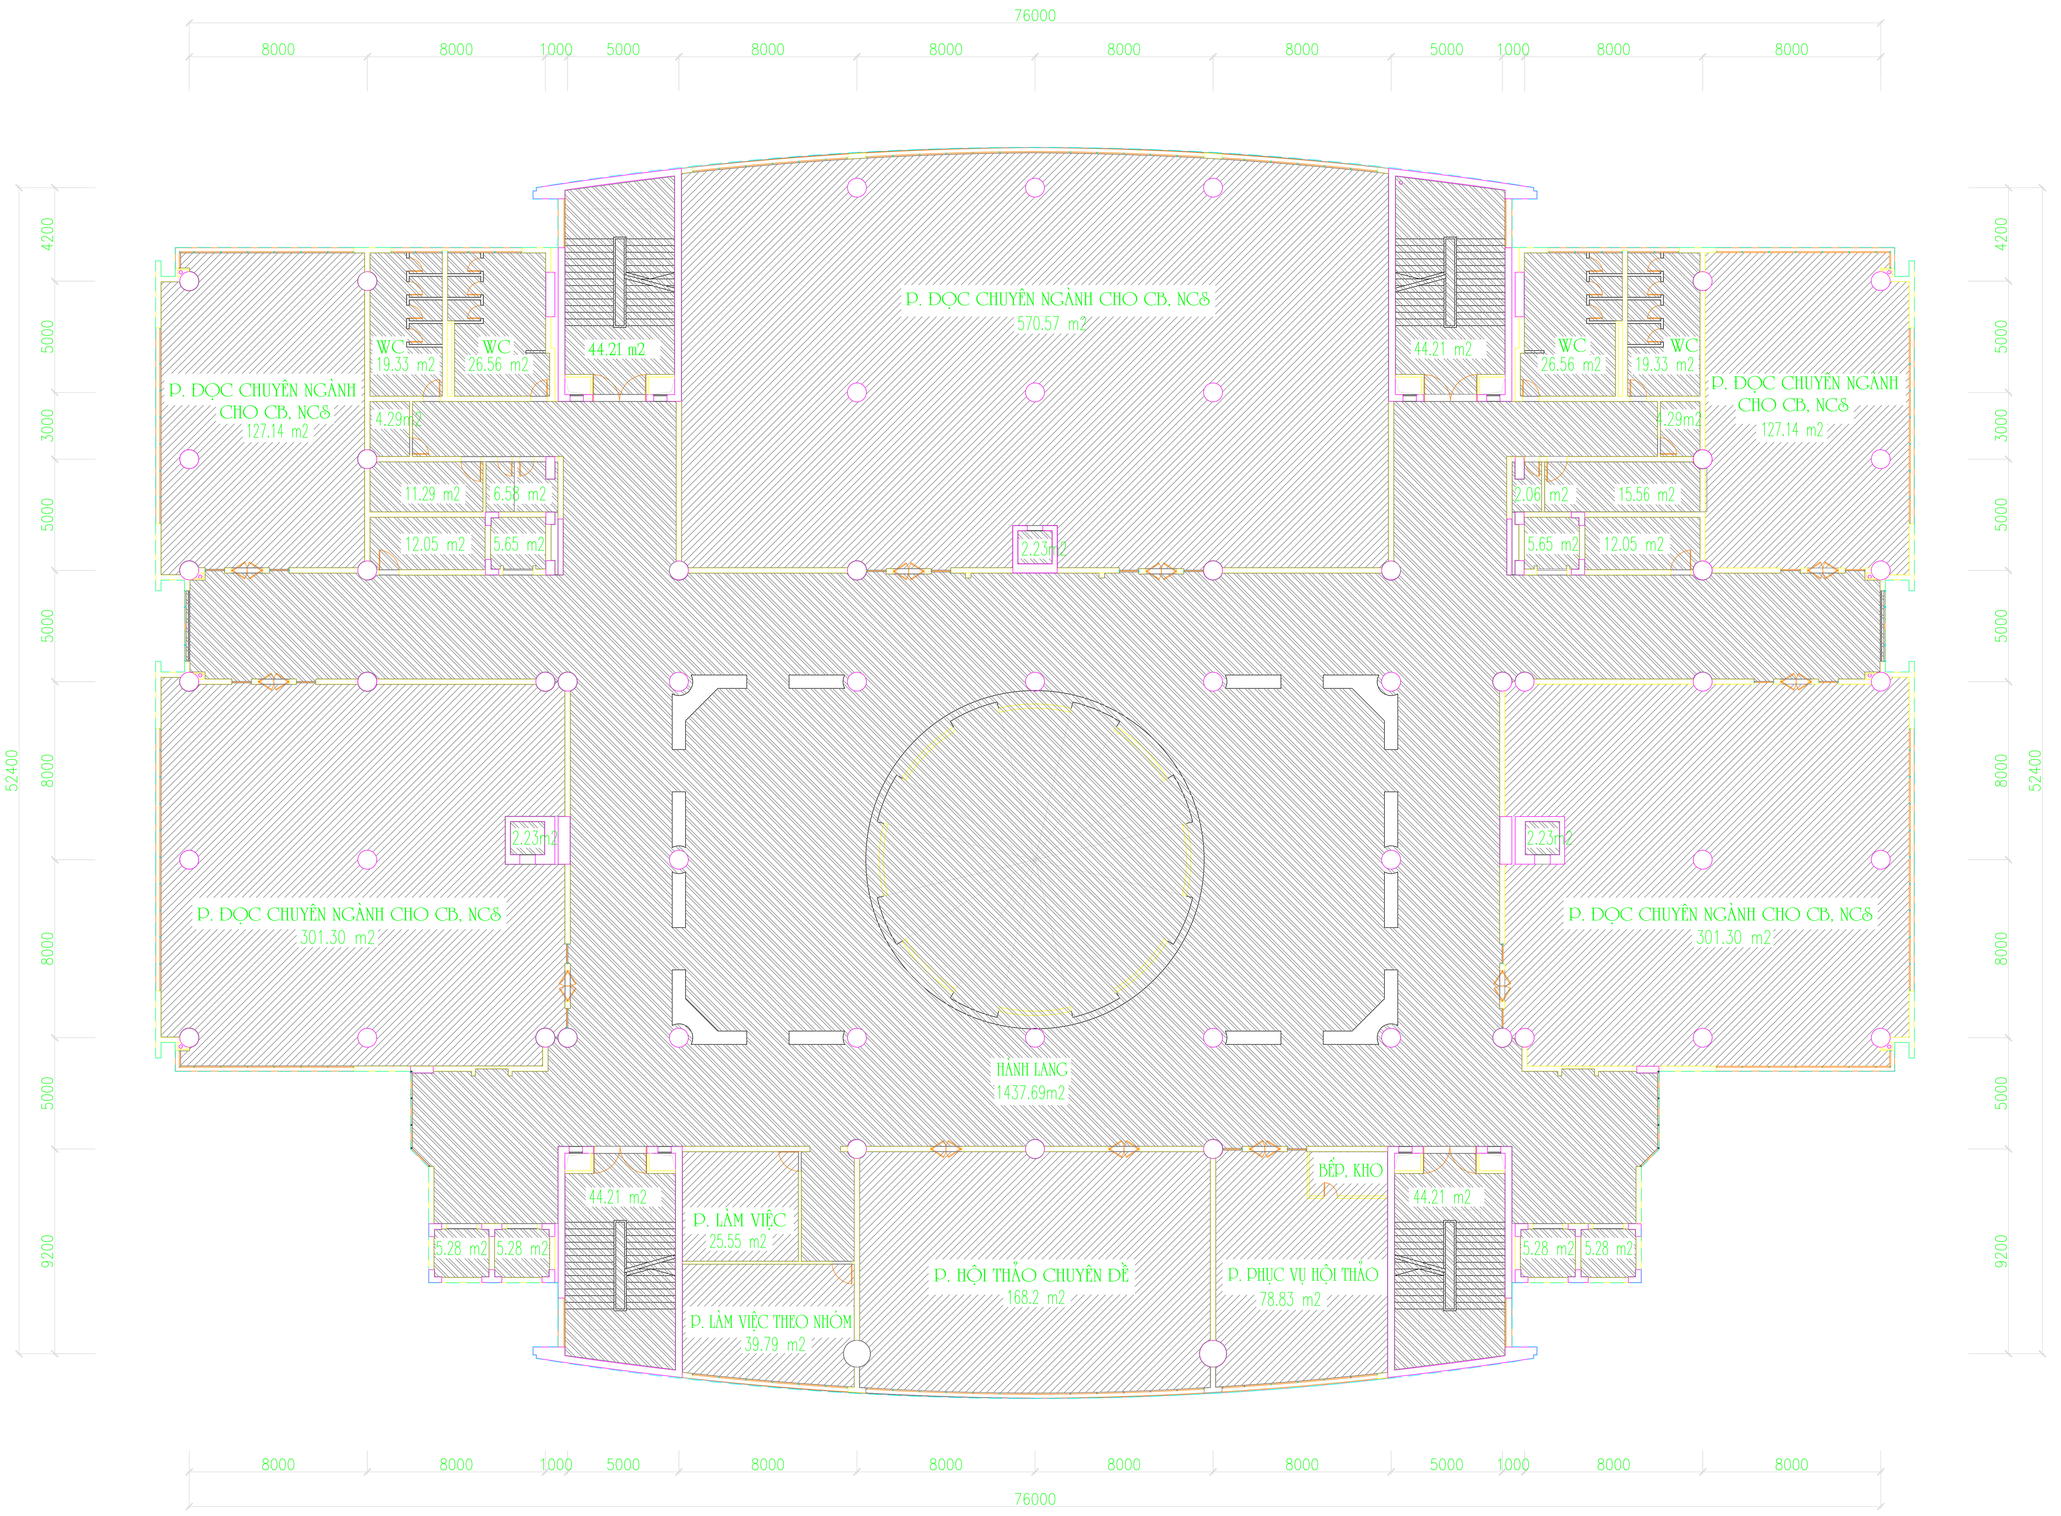

GHI CHÚ :

PHẦN ĐƯỢC TÍNH LÀ
DIỆN TÍCH SỬ DỤNG CHÍNH


PHẦN ĐƯỢC TÍNH LÀ
DIỆN TÍCH SỬ DỤNG PHỤ

MẶT BẰNG TẦNG 8

0(M) 1 3 6 10
THƯỚC TỈ LỆ

TẦNG 8 - THƯ VIỆN ĐIỆN TỬ TRƯỜNG ĐẠI HỌC BÁCH KHOA HÀ NỘI

DIỆN TÍCH XÂY DỰNG	DT SỬ DỤNG CHÍNH	DT SỬ DỤNG PHỤ	
		CẦU THANG, HÀNH LANG, SẢNH	KHU VỆ SINH VÀ KHO
3807.88 m2	1739.50 m2	1653.64 m2	159.95 m2
		1813.59 m2	

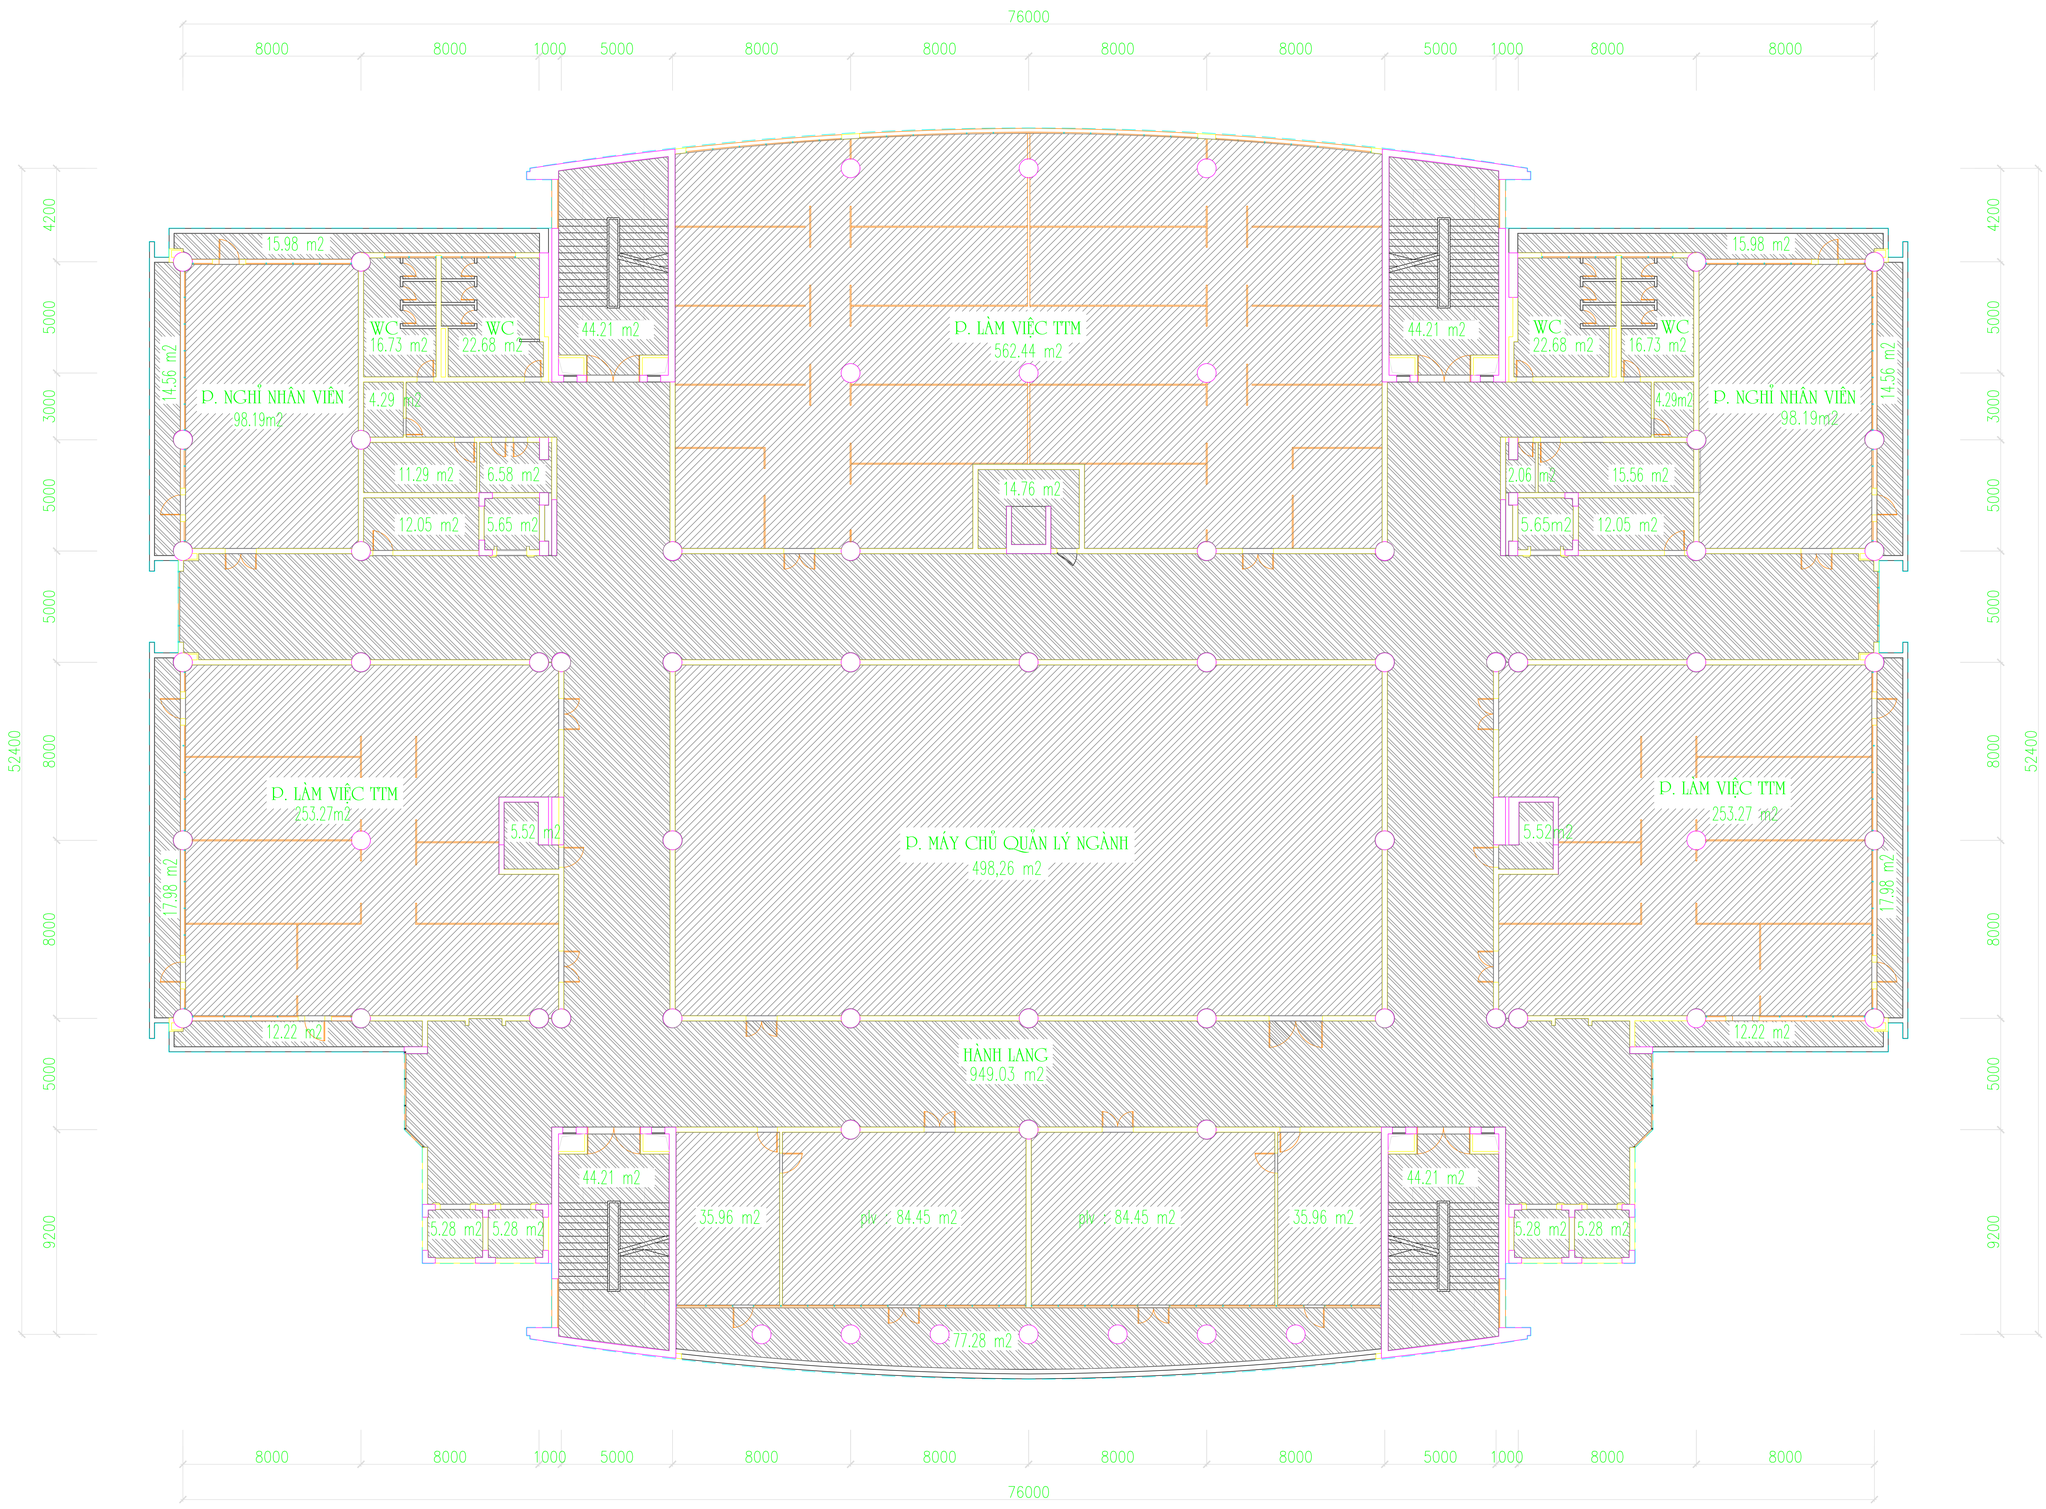

GHI CHÚ :

PHẦN ĐƯỢC TÍNH LÀ
DIỆN TÍCH SỬ DỤNG CHÍNH


PHẦN ĐƯỢC TÍNH LÀ
DIỆN TÍCH SỬ DỤNG PHỤ

MẶT BẰNG TẦNG 9

0(M) 1 3 6 10
THƯỚC TỈ LỆ

TẦNG 9 - THƯ VIỆN ĐIỆN TỬ TRƯỜNG ĐẠI HỌC BÁCH KHOA HÀ NỘI

DIỆN TÍCH XÂY DỰNG	DT SỬ DỤNG CHÍNH	DT SỬ DỤNG PHỤ	
		CẦU THANG, HÀNH LANG, SẢNH	KHU VỆ SINH VÀ KHO
3807.88 m2	2004.44 m2	1382.85 m2	130.26 m2
		1513.11 m2	

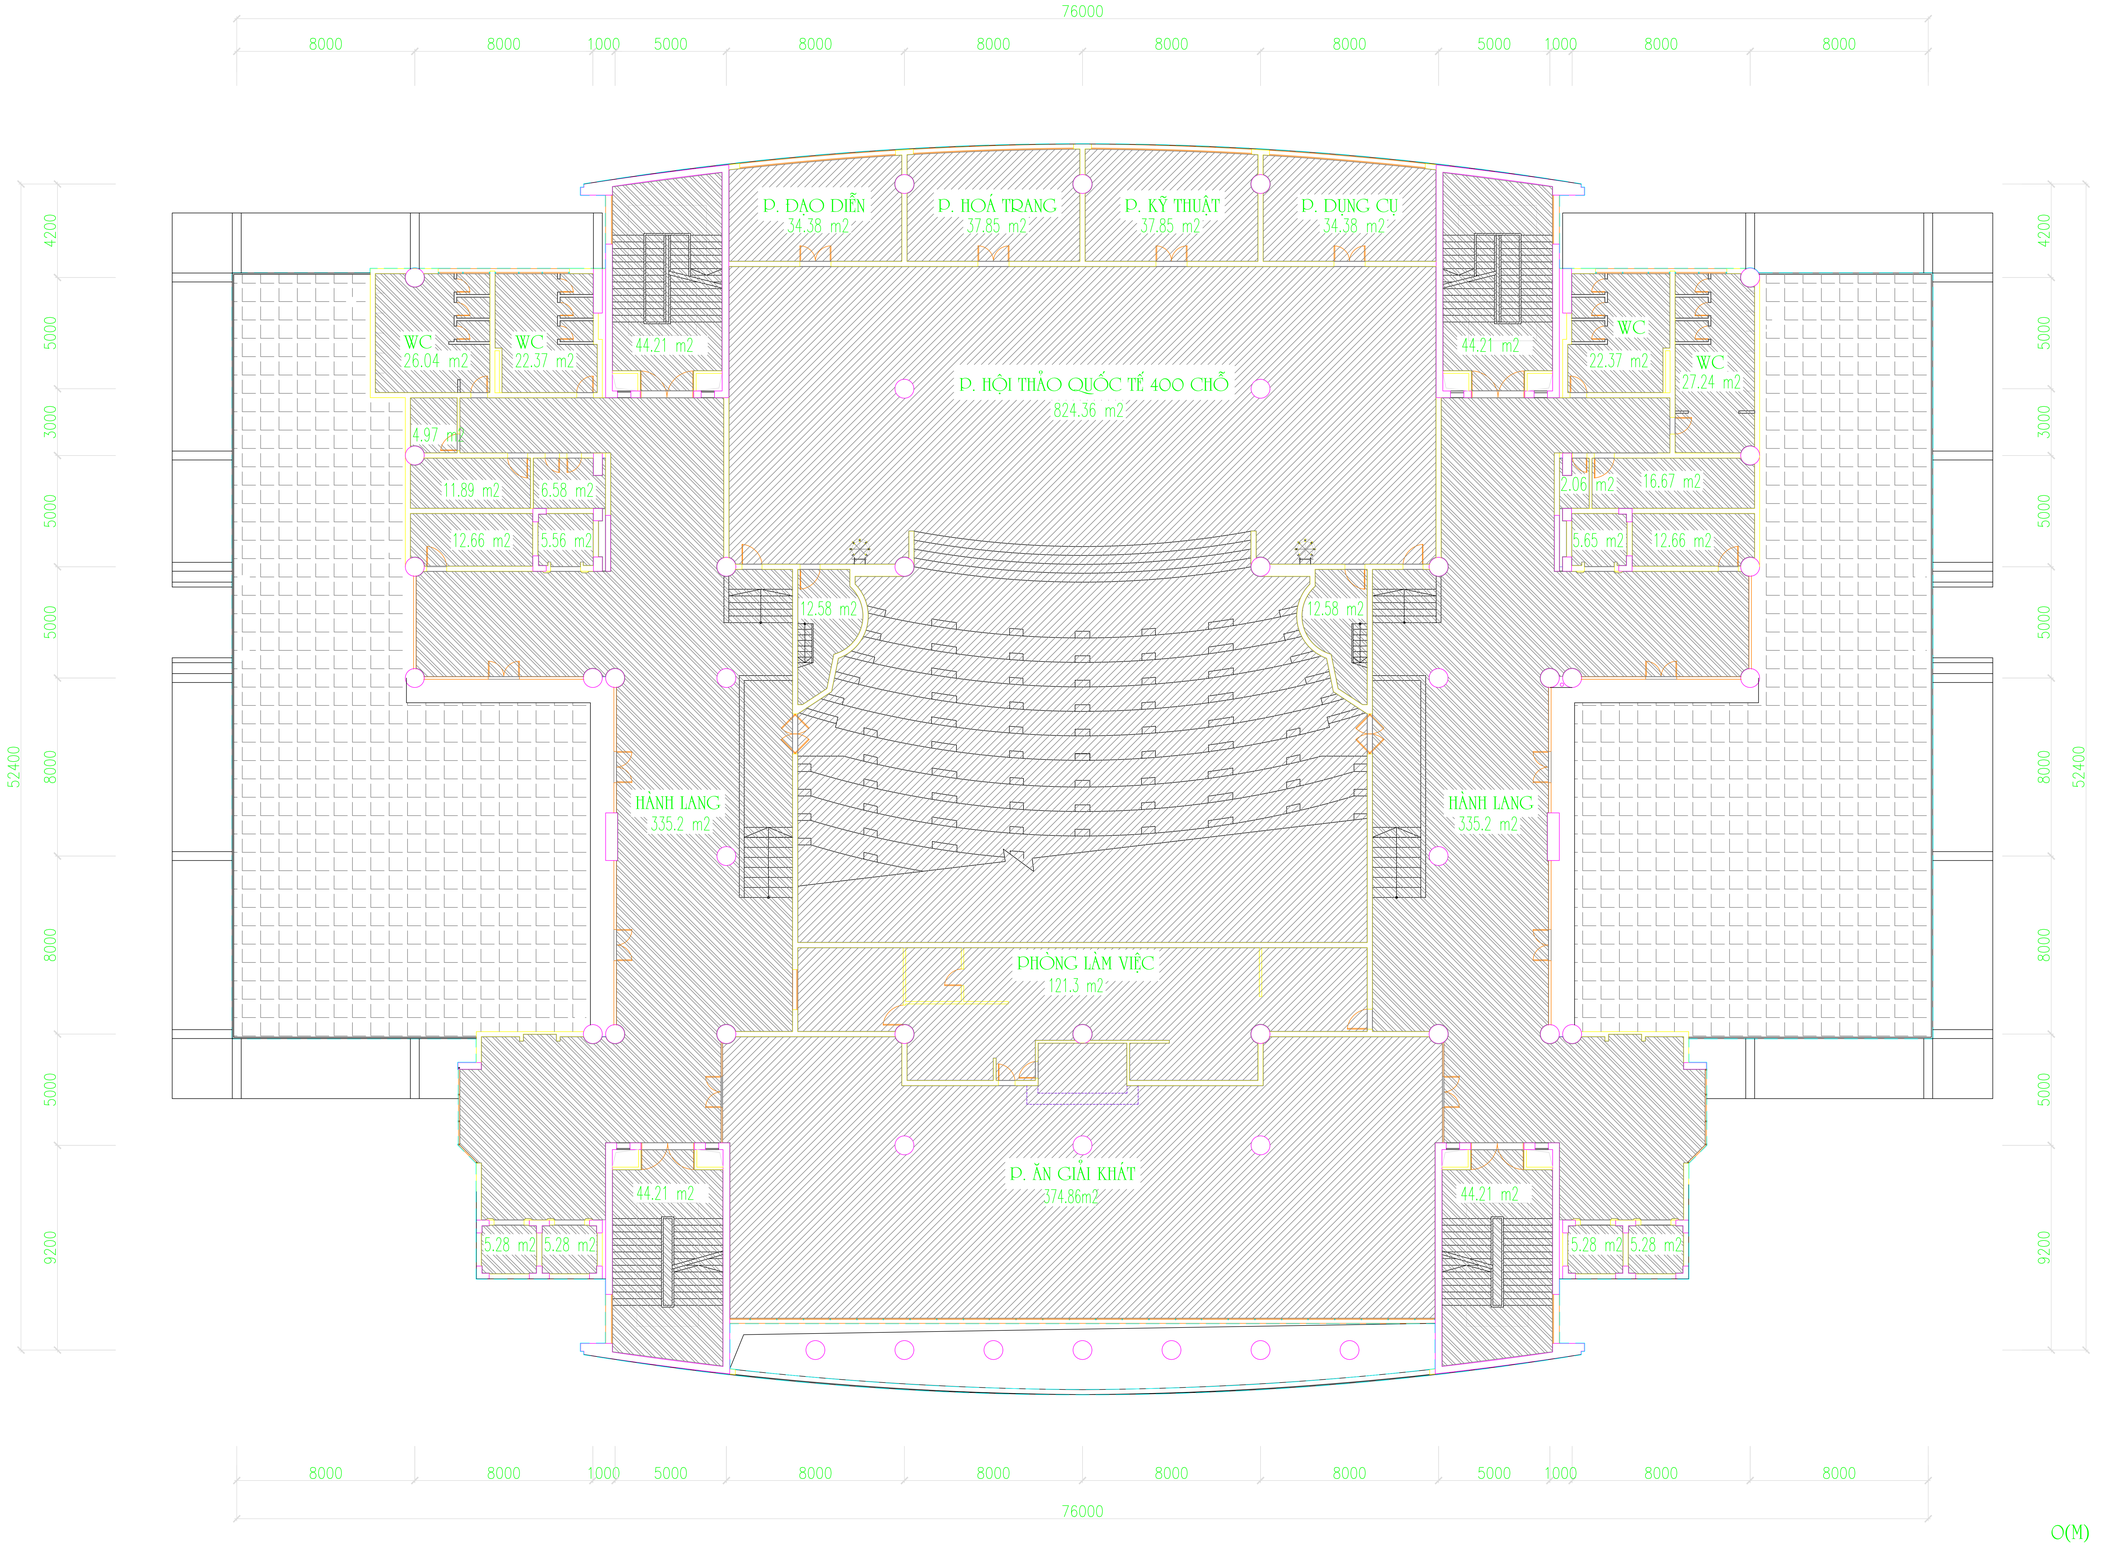

GHI CHÚ :

PHẦN ĐƯỢC TÍNH LÀ
DIỆN TÍCH SỬ DỤNG CHÍNH


PHẦN ĐƯỢC TÍNH LÀ
DIỆN TÍCH SỬ DỤNG PHỤ

MẶT BẰNG TẦNG 10 (CAO ĐỘ +40.20)

THƯỚC TỈ LỆ 0(M) 1 3 6 10

TẦNG 10 (CAO ĐỘ +40.20) - THƯ VIỆN ĐIỆN TỬ TRƯỜNG ĐẠI HỌC BÁCH KHOA HÀ NỘI

DIỆN TÍCH XÂY DỰNG	DT SỬ DỤNG CHÍNH	DT SỬ DỤNG PHỤ	
		CẦU THANG, HÀNH LANG, SẢNH	KHU VỆ SINH VÀ KHO
3574.26 m2	1464.98 m2	904.82 m2	165.51 m2
		1070.33 m2	

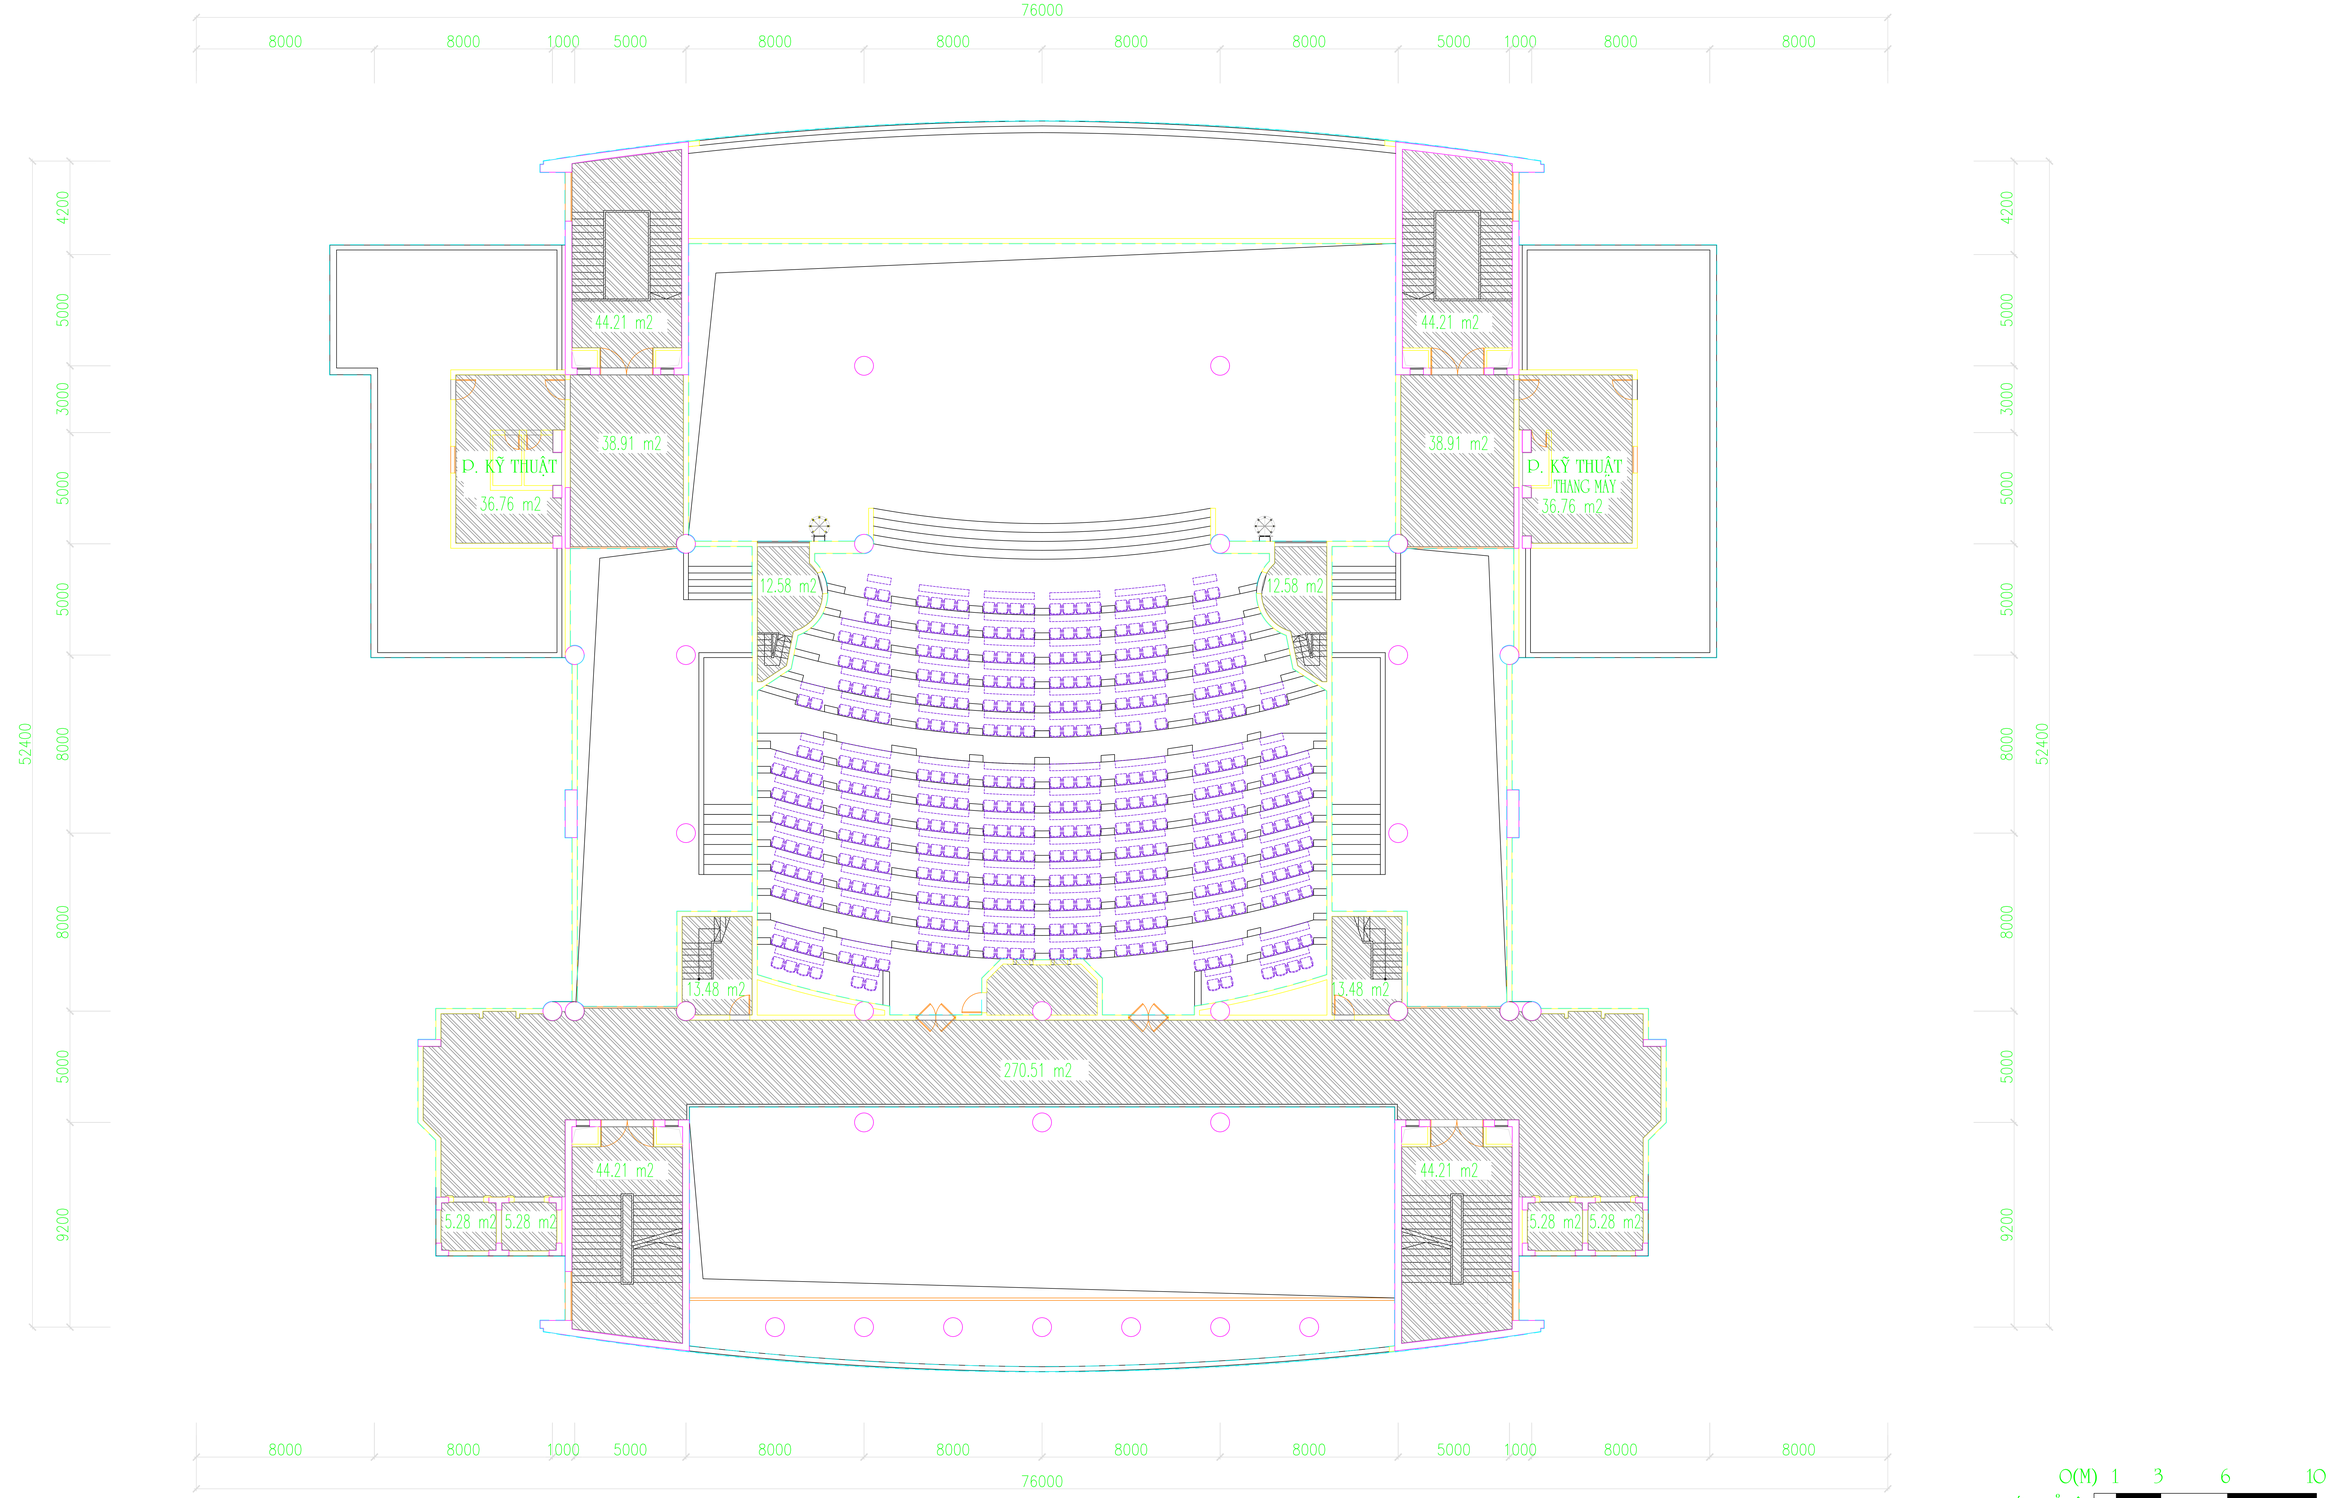

O(M) 1 3 6 10

THƯỚC TỈ LỆ


GHI CHÚ :

PHẦN ĐƯỢC TÍNH LÀ DIỆN TÍCH SỬ DỤNG PHỤ

MẶT BẰNG TẦNG 10 (CAO ĐỘ +43.80)

TẦNG 10 (CAO ĐỘ +43.80) - THƯ VIỆN ĐIỆN TỬ TRƯỜNG ĐẠI HỌC BÁCH KHOA HÀ NỘI

DIỆN TÍCH XÂY DỰNG	DT SỬ DỤNG CHÍNH	DT SỬ DỤNG PHỤ	
		CẦU THANG, HÀNH LANG, SẢNH	KHU VỆ SINH VÀ KHO
1267.92 m2	0.00 m2	671.93 m2	0.00 m2
		671.93 m2	

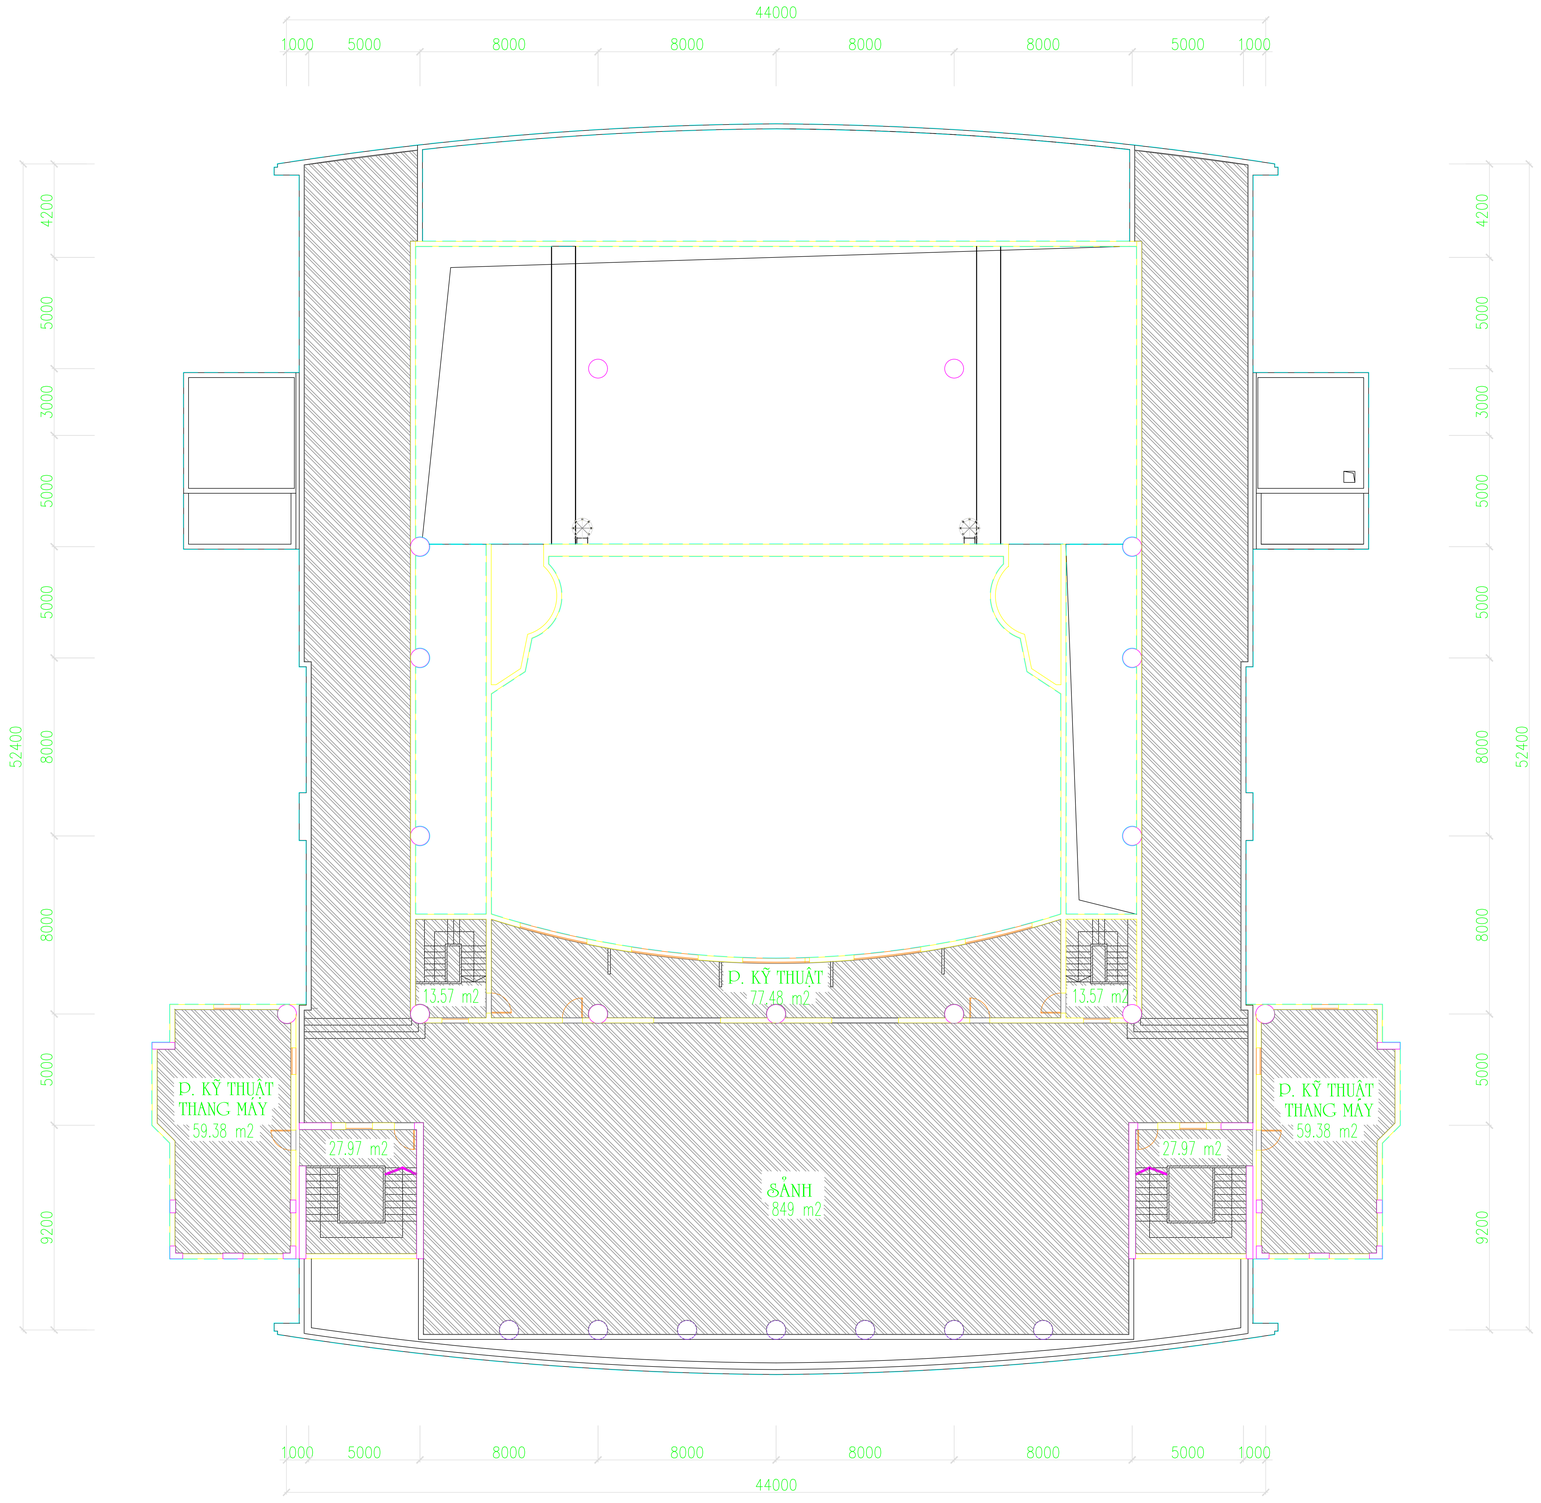

0(M) 1 3 6 10

THƯỚC TỈ LỆ


GHI CHÚ :

PHẦN ĐƯỢC TÍNH LÀ DIỆN TÍCH SỬ DỤNG PHỤ

MẶT BẰNG TẦNG 10 (CAO ĐỘ +47.40)

TẦNG 10 (CAO ĐỘ +47.40) - THƯ VIỆN ĐIỆN TỬ TRƯỜNG ĐẠI HỌC BÁCH KHOA HÀ NỘI

DIỆN TÍCH XÂY DỰNG	DT SỬ DỤNG CHÍNH	DT SỬ DỤNG PHỤ	
		CẦU THANG, HÀNH LANG, SẢNH	KHU VỆ SINH VÀ KHO
1477.88 m2	0.00 m2	1128.32 m2	0.00 m2
		1128.32 m2	

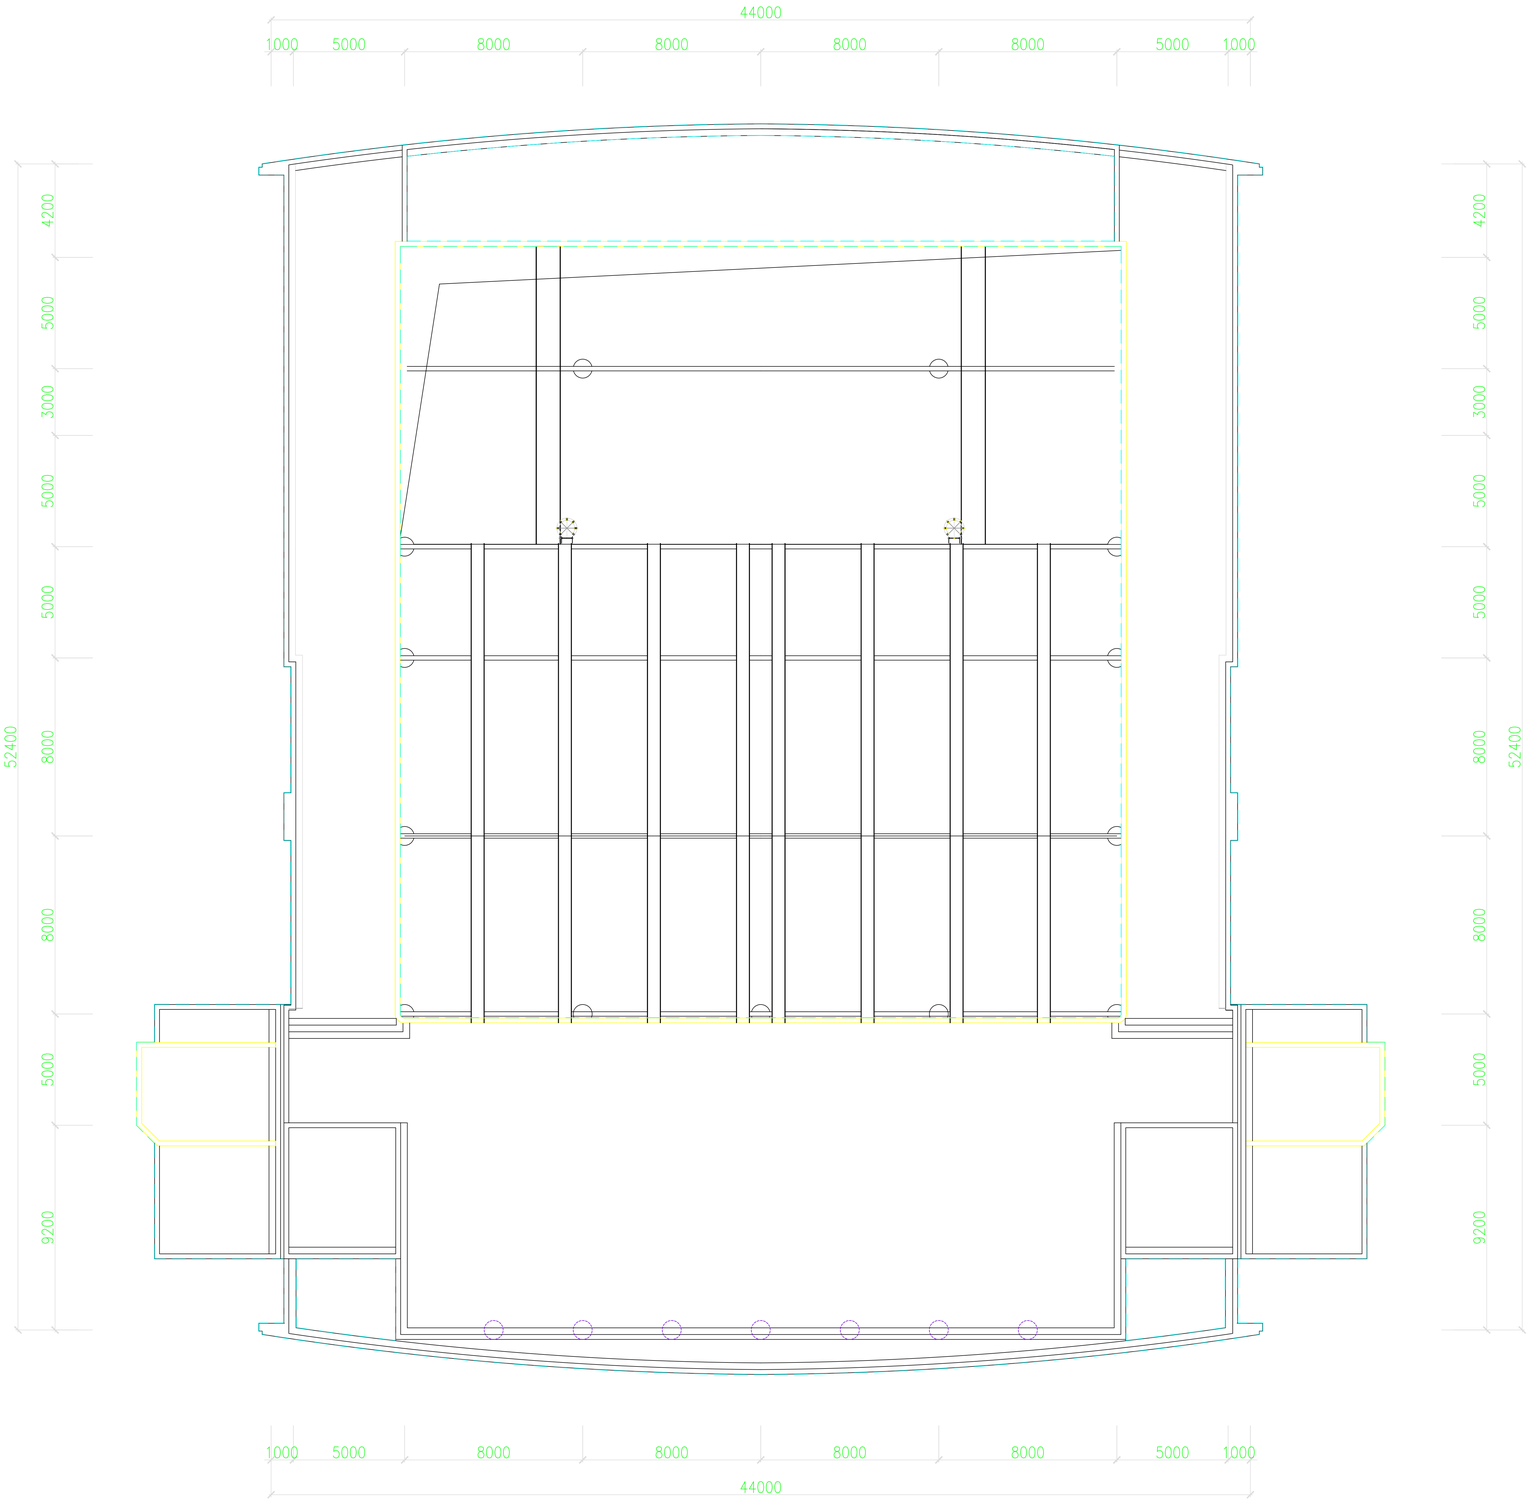

MẶT BẰNG TẦNG 10 (CAO ĐỘ +51.13)

O(M) 1 3 6 10

THƯỚC TỈ LỆ

TẦNG 10 TẦNG 10 (CAO ĐỘ +51.13) - THƯ VIỆN ĐIỆN TỬ TRƯỜNG ĐẠI HỌC BÁCH KHOA HÀ NỘI

DIỆN TÍCH XÂY DỰNG	DT SỬ DỤNG CHÍNH	DT SỬ DỤNG PHỤ	
		CẦU THANG, HÀNH LANG, SẢNH	KHU VỆ SINH VÀ KHO
1203.85 m2	0.00 m2	0.00 m2	0.00 m2
		0.00 m2	

THƯ VIỆN ĐIỆN TỬ TRƯỜNG ĐẠI HỌC BÁCH KHOA HÀ NỘI

BẢNG THỐNG KÊ DIỆN TÍCH NHÀ

THƯ VIỆN ĐIỆN TỬ TRƯỜNG ĐẠI HỌC BÁCH KHOA HÀ NỘI

KH / ST	DIỆN TÍCH XÂY DỰNG	DT SỬ DỤNG CHÍNH (S1)	DT SỬ DỤNG PHỤ (S2)		KH / ST	DIỆN TÍCH XÂY DỰNG	DT SỬ DỤNG CHÍNH (S1)	DT SỬ DỤNG PHỤ (S2)	
TẦNG 1	4586.19 m2	1390.38 m2	CẦU THANG, HÀNH LANG, SẢNH	KHU VỆ SINH VÀ KHO	TẦNG 9	3807.88 m2	2004.44 m2	HÀNH LANG, SẢNH, CẦU THANG	KHU VỆ SINH VÀ KHO
			2087.92 m2	148.09 m2				1382.85 m2	130.26 m2
			2236.01 m2					1513.11 m2	
TẦNG 2	3719.54 m2	1808.32 m2	HÀNH LANG, SẢNH, CẦU THANG	KHU VỆ SINH VÀ KHO	TẦNG 10 (CAO ĐỘ +40.20)	3574.26 m2	1464.98 m2	CẦU THANG, HÀNH LANG, SẢNH	KHU VỆ SINH VÀ KHO
			1344.36m2	159.95 m2				904.82 m2	165.51 m2
			1504.31m2					1070.33 m2	
TẦNG 3	3550.89 m2	1847.77 m2	HÀNH LANG, SẢNH, CẦU THANG	KHU VỆ SINH VÀ KHO	TẦNG 10 (CAO ĐỘ +41.80)	1267.92 m2	0.00 m2	HÀNH LANG, SẢNH, CẦU THANG	KHU VỆ SINH VÀ KHO
			1235.23m2	159.95m2				671.93 m2	0.00 m2
			1395.18m2					671.93 m2	
TẦNG 4	3550.89 m2	1760.07 m2	HÀNH LANG, SẢNH, CẦU THANG	KHU VỆ SINH VÀ KHO	TẦNG 10 (CAO ĐỘ +47.40)	1477.88 m2	0.00 m2	HÀNH LANG, SẢNH, CẦU THANG	KHU VỆ SINH VÀ KHO
			1309.23m2	159.95 m2				1128.32 m2	0.00 m2
			1469.18m2					1128.32 m2	
TẦNG 5	3408.03 m2	1718.55 m2	HÀNH LANG, SẢNH, CẦU THANG	KHU VỆ SINH VÀ KHO	TẦNG 10 (CAO ĐỘ +51.15)	1203.85 m2	0.00 m2	HÀNH LANG, SẢNH, CẦU THANG	KHU VỆ SINH VÀ KHO
			1234.42m2	159.95 m2				0.00 m2	0.00 m2
			1394.37m2					0.00 m2	
TẦNG 6	3807.88 m2	1718.05 m2	HÀNH LANG, SẢNH, CẦU THANG	KHU VỆ SINH VÀ KHO	TẦNG 10 (CAO ĐỘ +51.15)	0.00 m2	0.00 m2	HÀNH LANG, SẢNH, CẦU THANG	KHU VỆ SINH VÀ KHO
			1670.17 m2	159.95 m2				0.00 m2	0.00 m2
			1830.12 m2					0.00 m2	
TẦNG 7	3807.88 m2	1739.50m2	HÀNH LANG, SẢNH, CẦU THANG	KHU VỆ SINH VÀ KHO	TOÀN TẦNG	41570.97 m2	17191.56 m2	17840.04 m2	
			1653.64 m2	159.95 m2					
			1813.59 m2						
TẦNG 8	3807.88 m2	1739.50 m2	HÀNH LANG, SẢNH, CẦU THANG	KHU VỆ SINH VÀ KHO	DIỆN TÍCH SỬ DỤNG TOÀN NHÀ S = S1+ S2= 17191.56 + 17840.04 = 35031.60 m2				
			1653.64 m2	159.95 m2					
			1813.59 m2						